


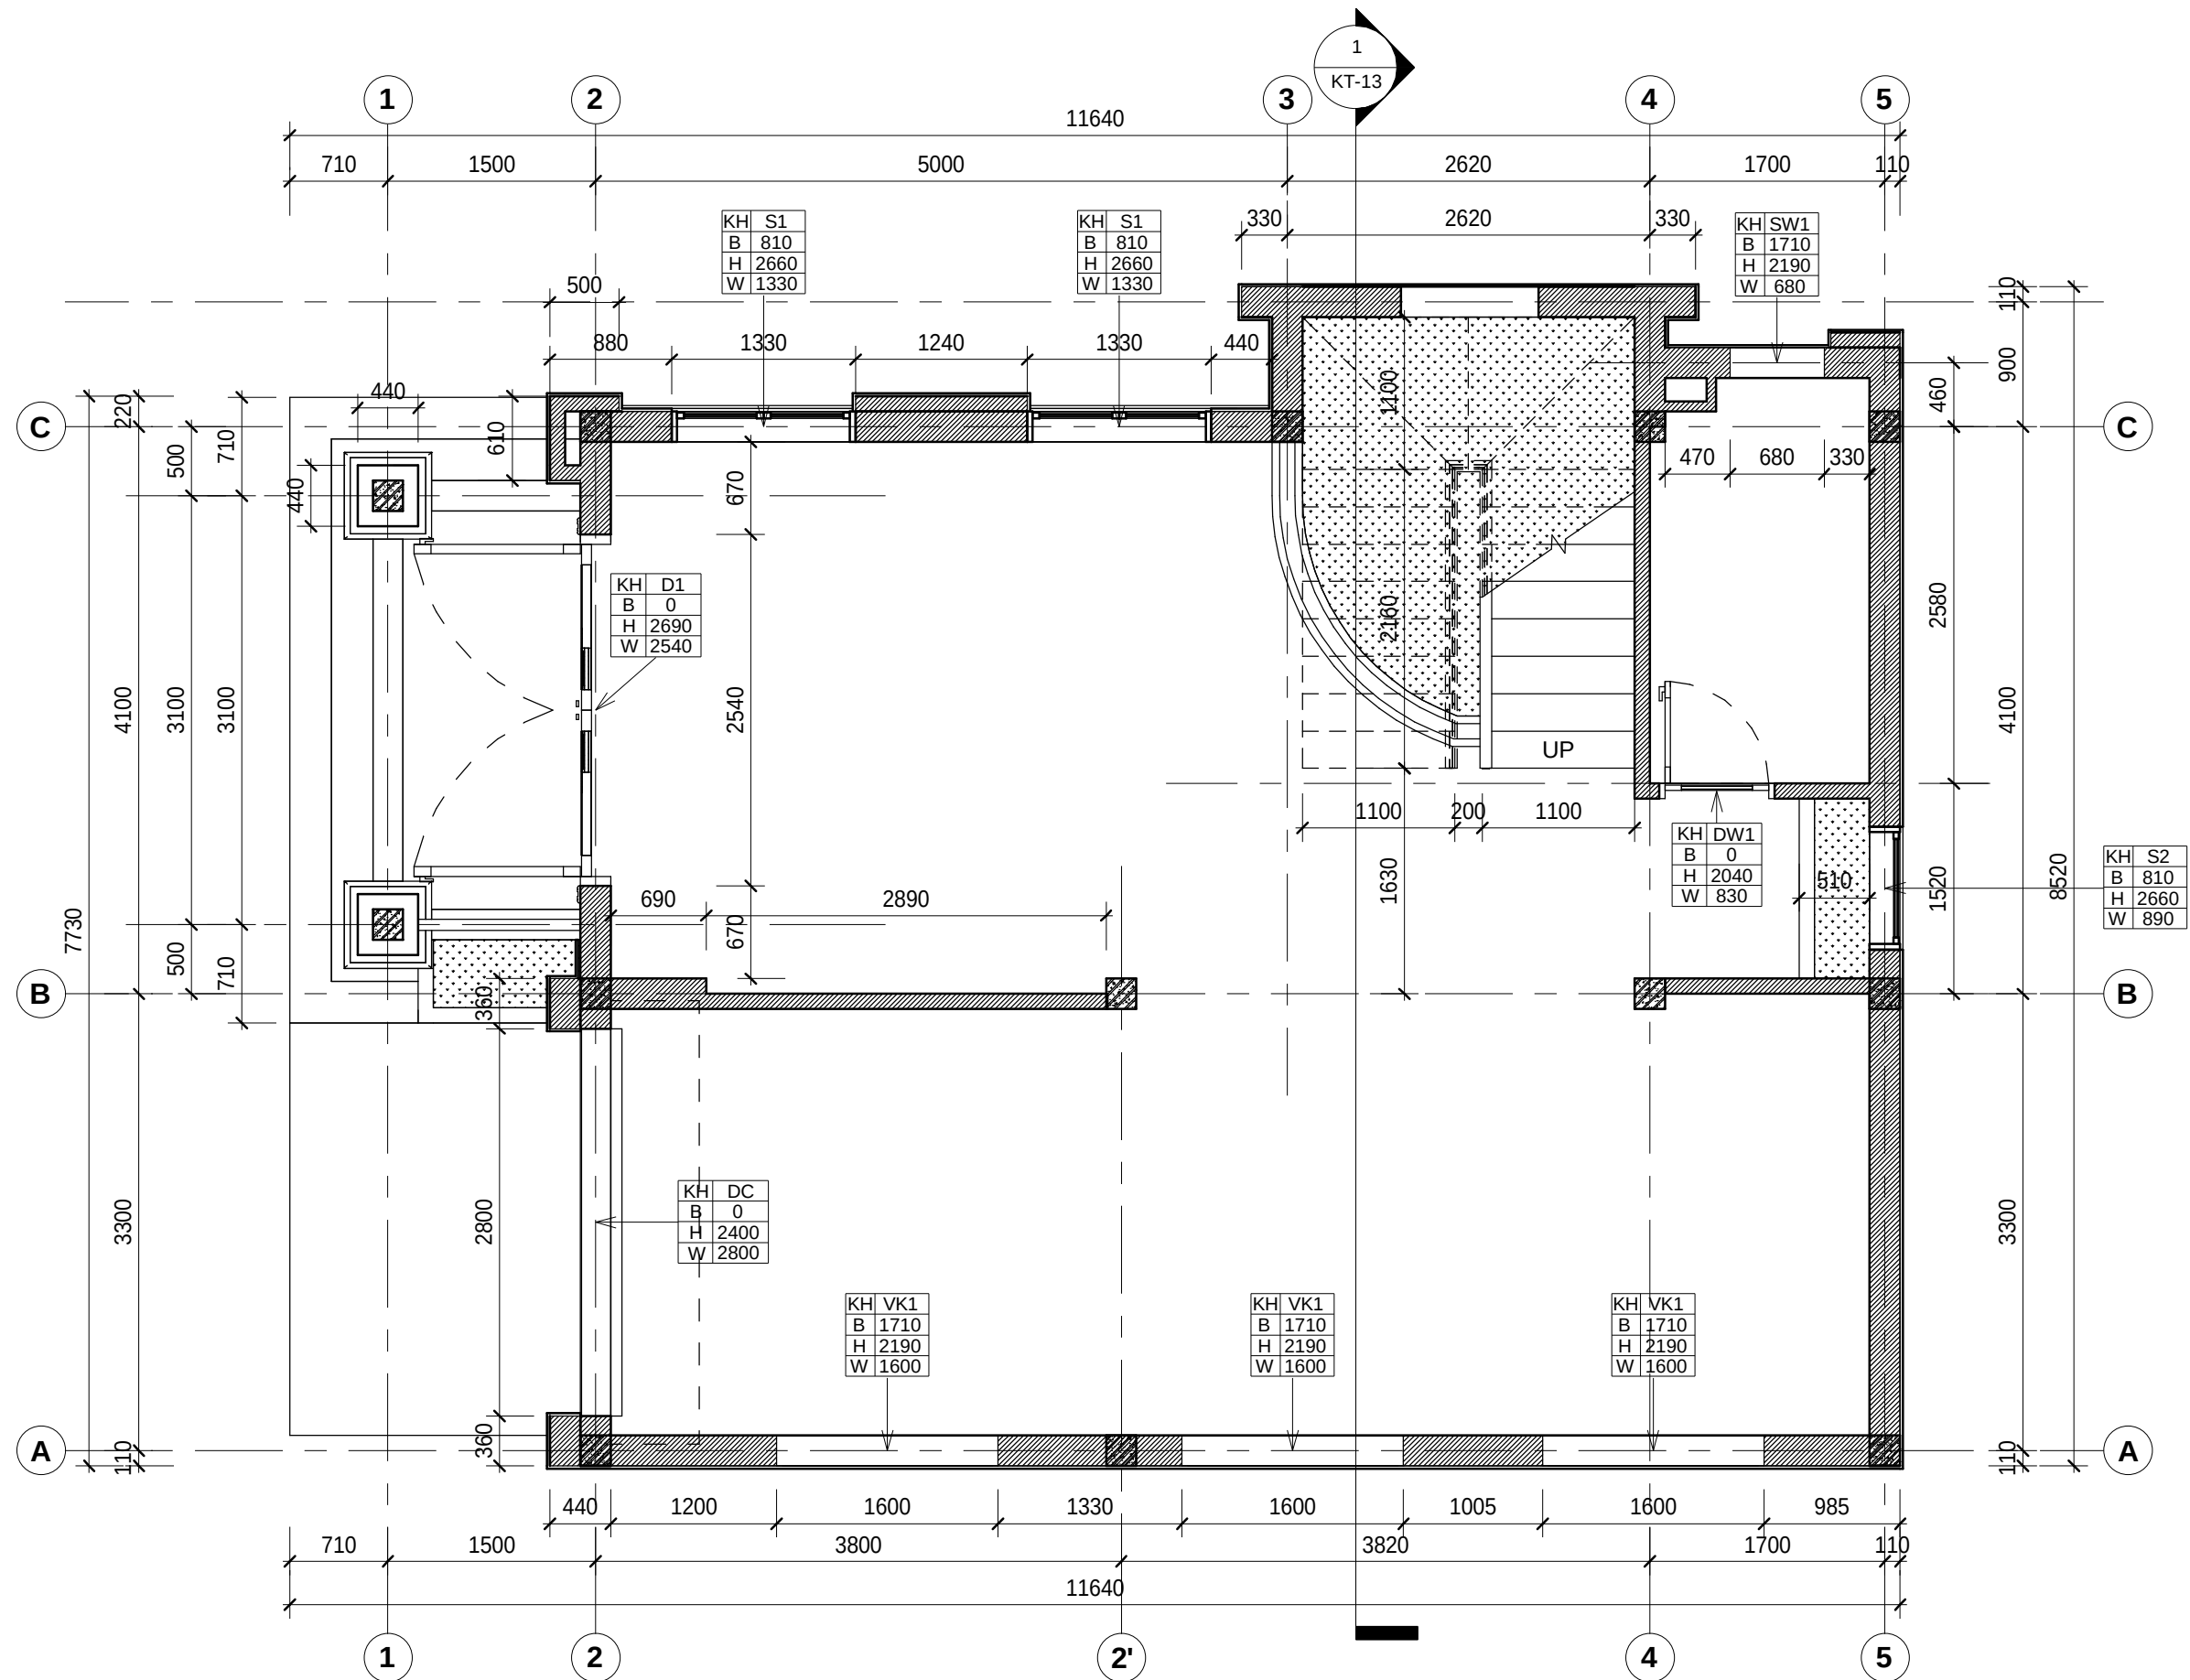


GHI CHÚ

-Toàn bộ cửa được tính khuôn 4, riêng cửa đi chính bằng khuôn gỗ 6


MẶT BẰNG BỐ TRÍ CỬA TẦNG 1


KT-01

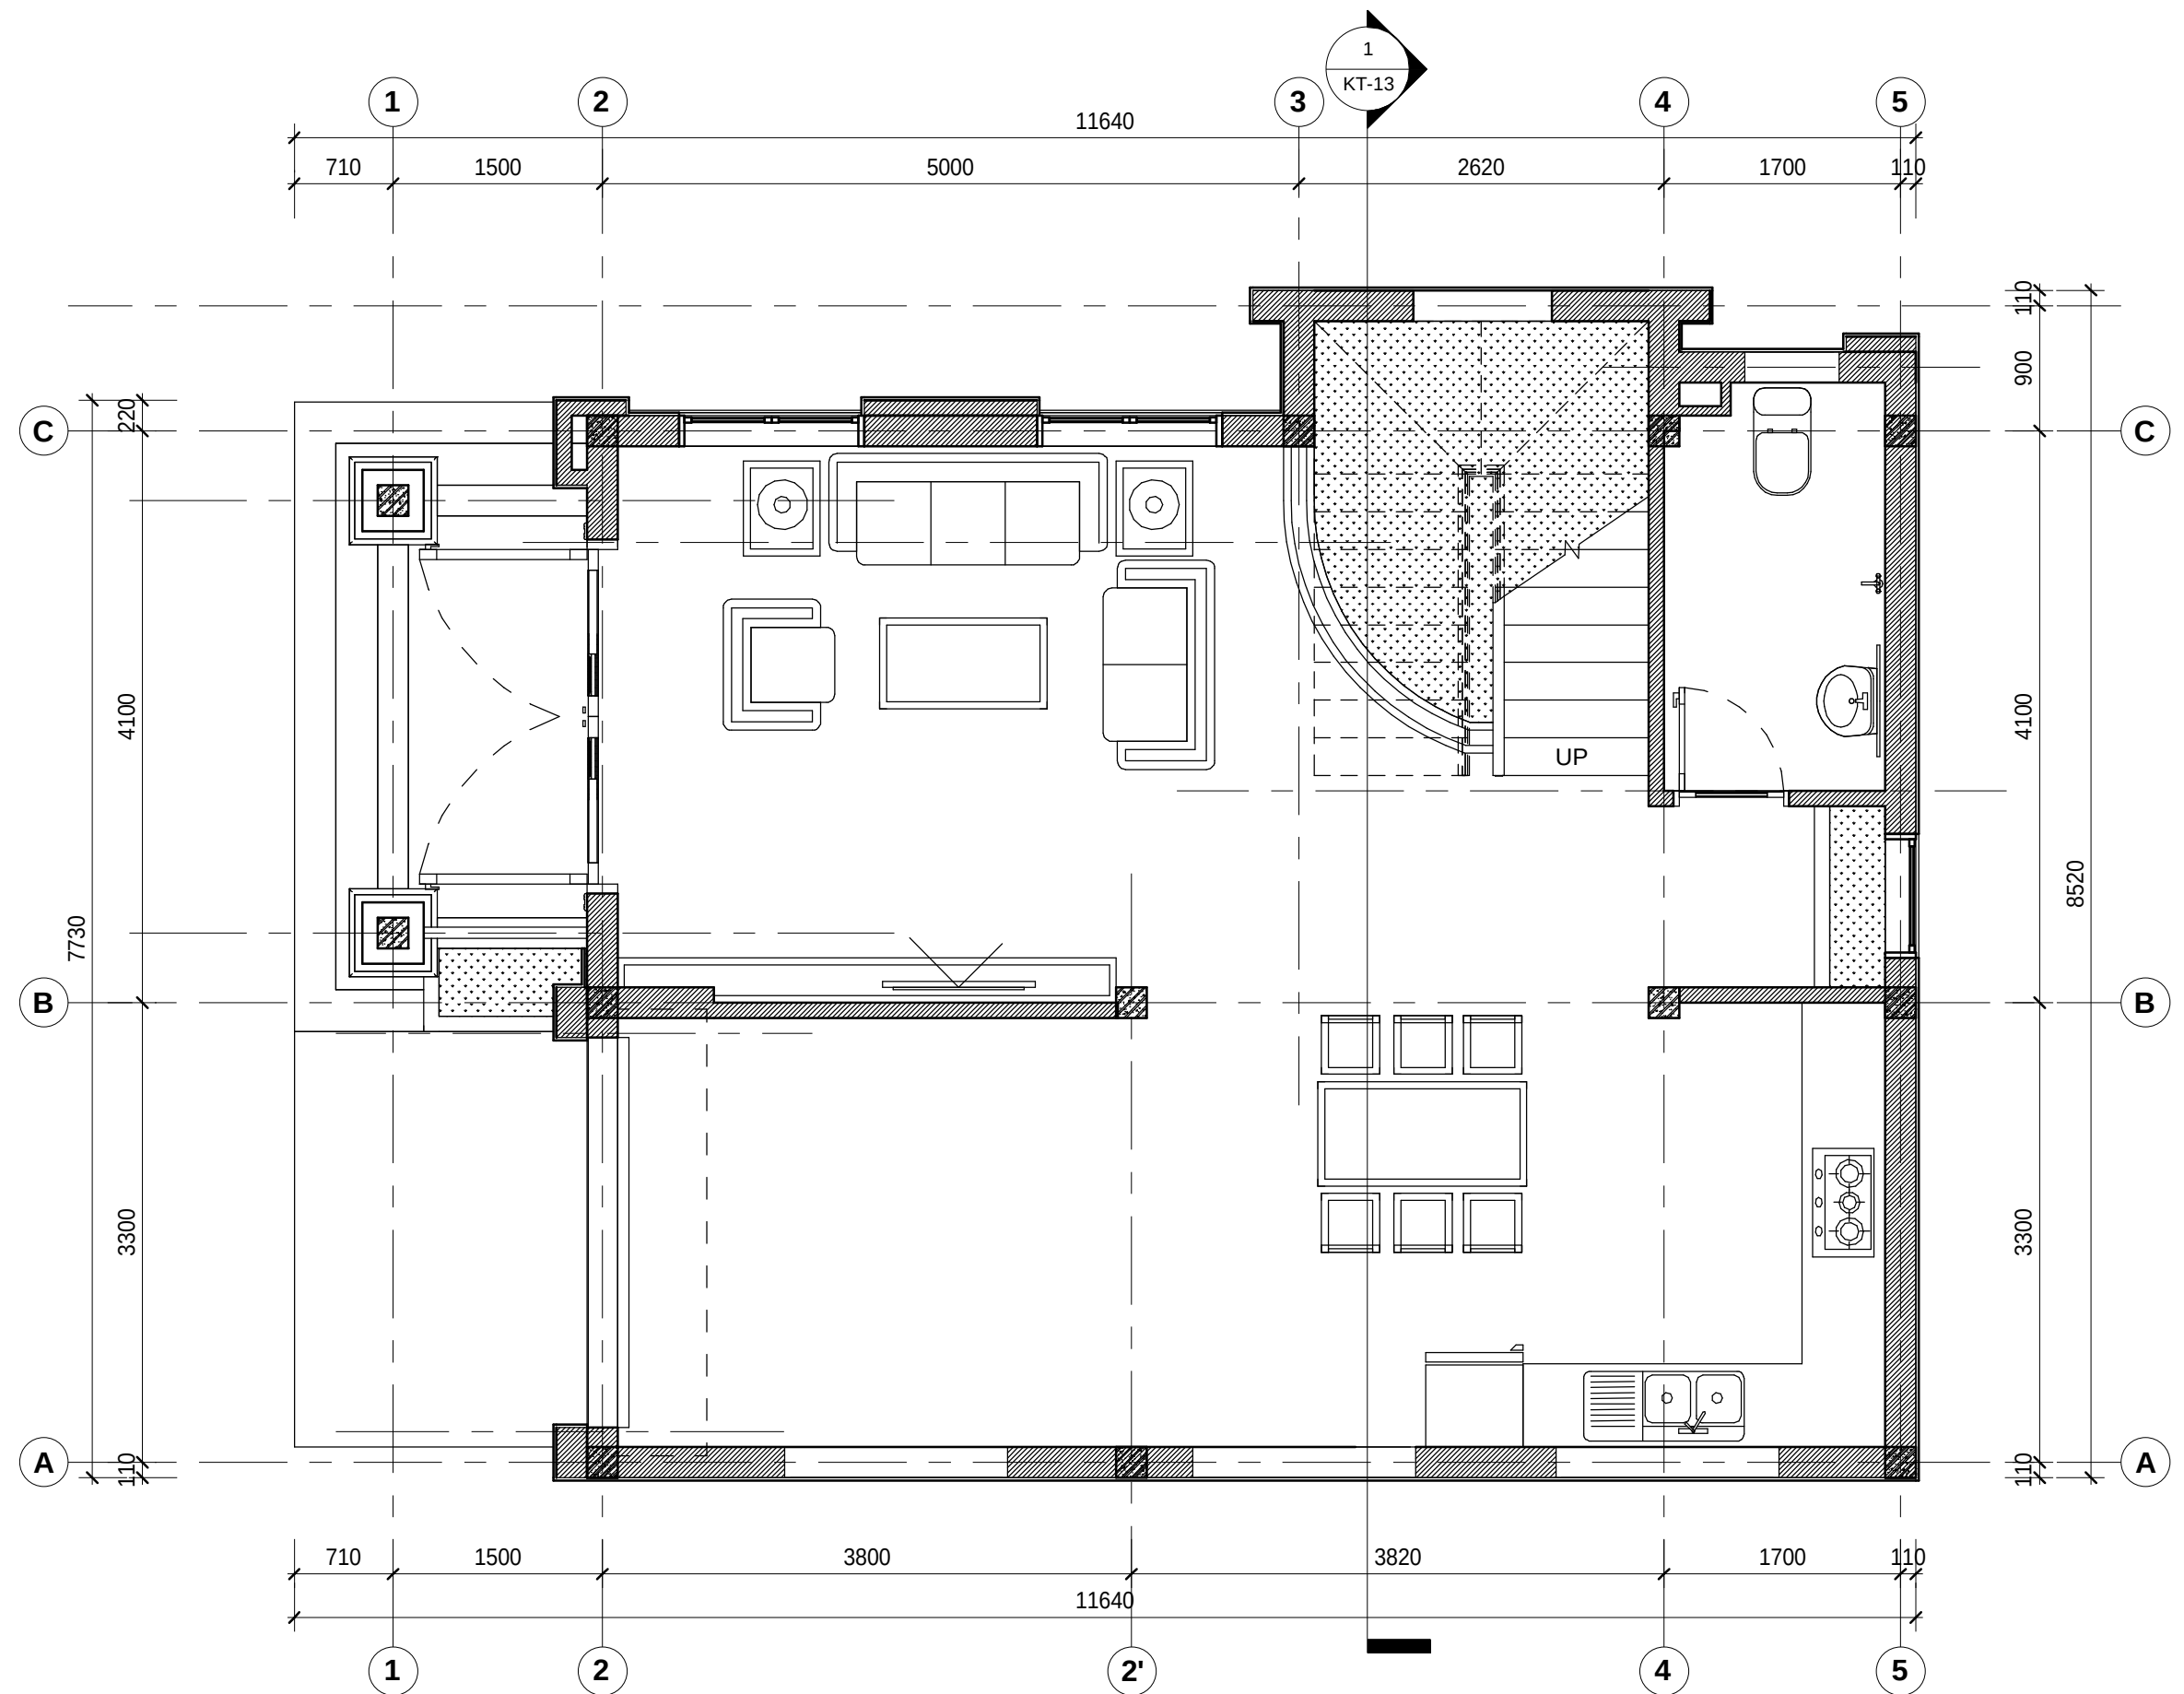


MẶT BẰNG BỐ TRÍ NỘI THẤT TẦNG 1


KT-02

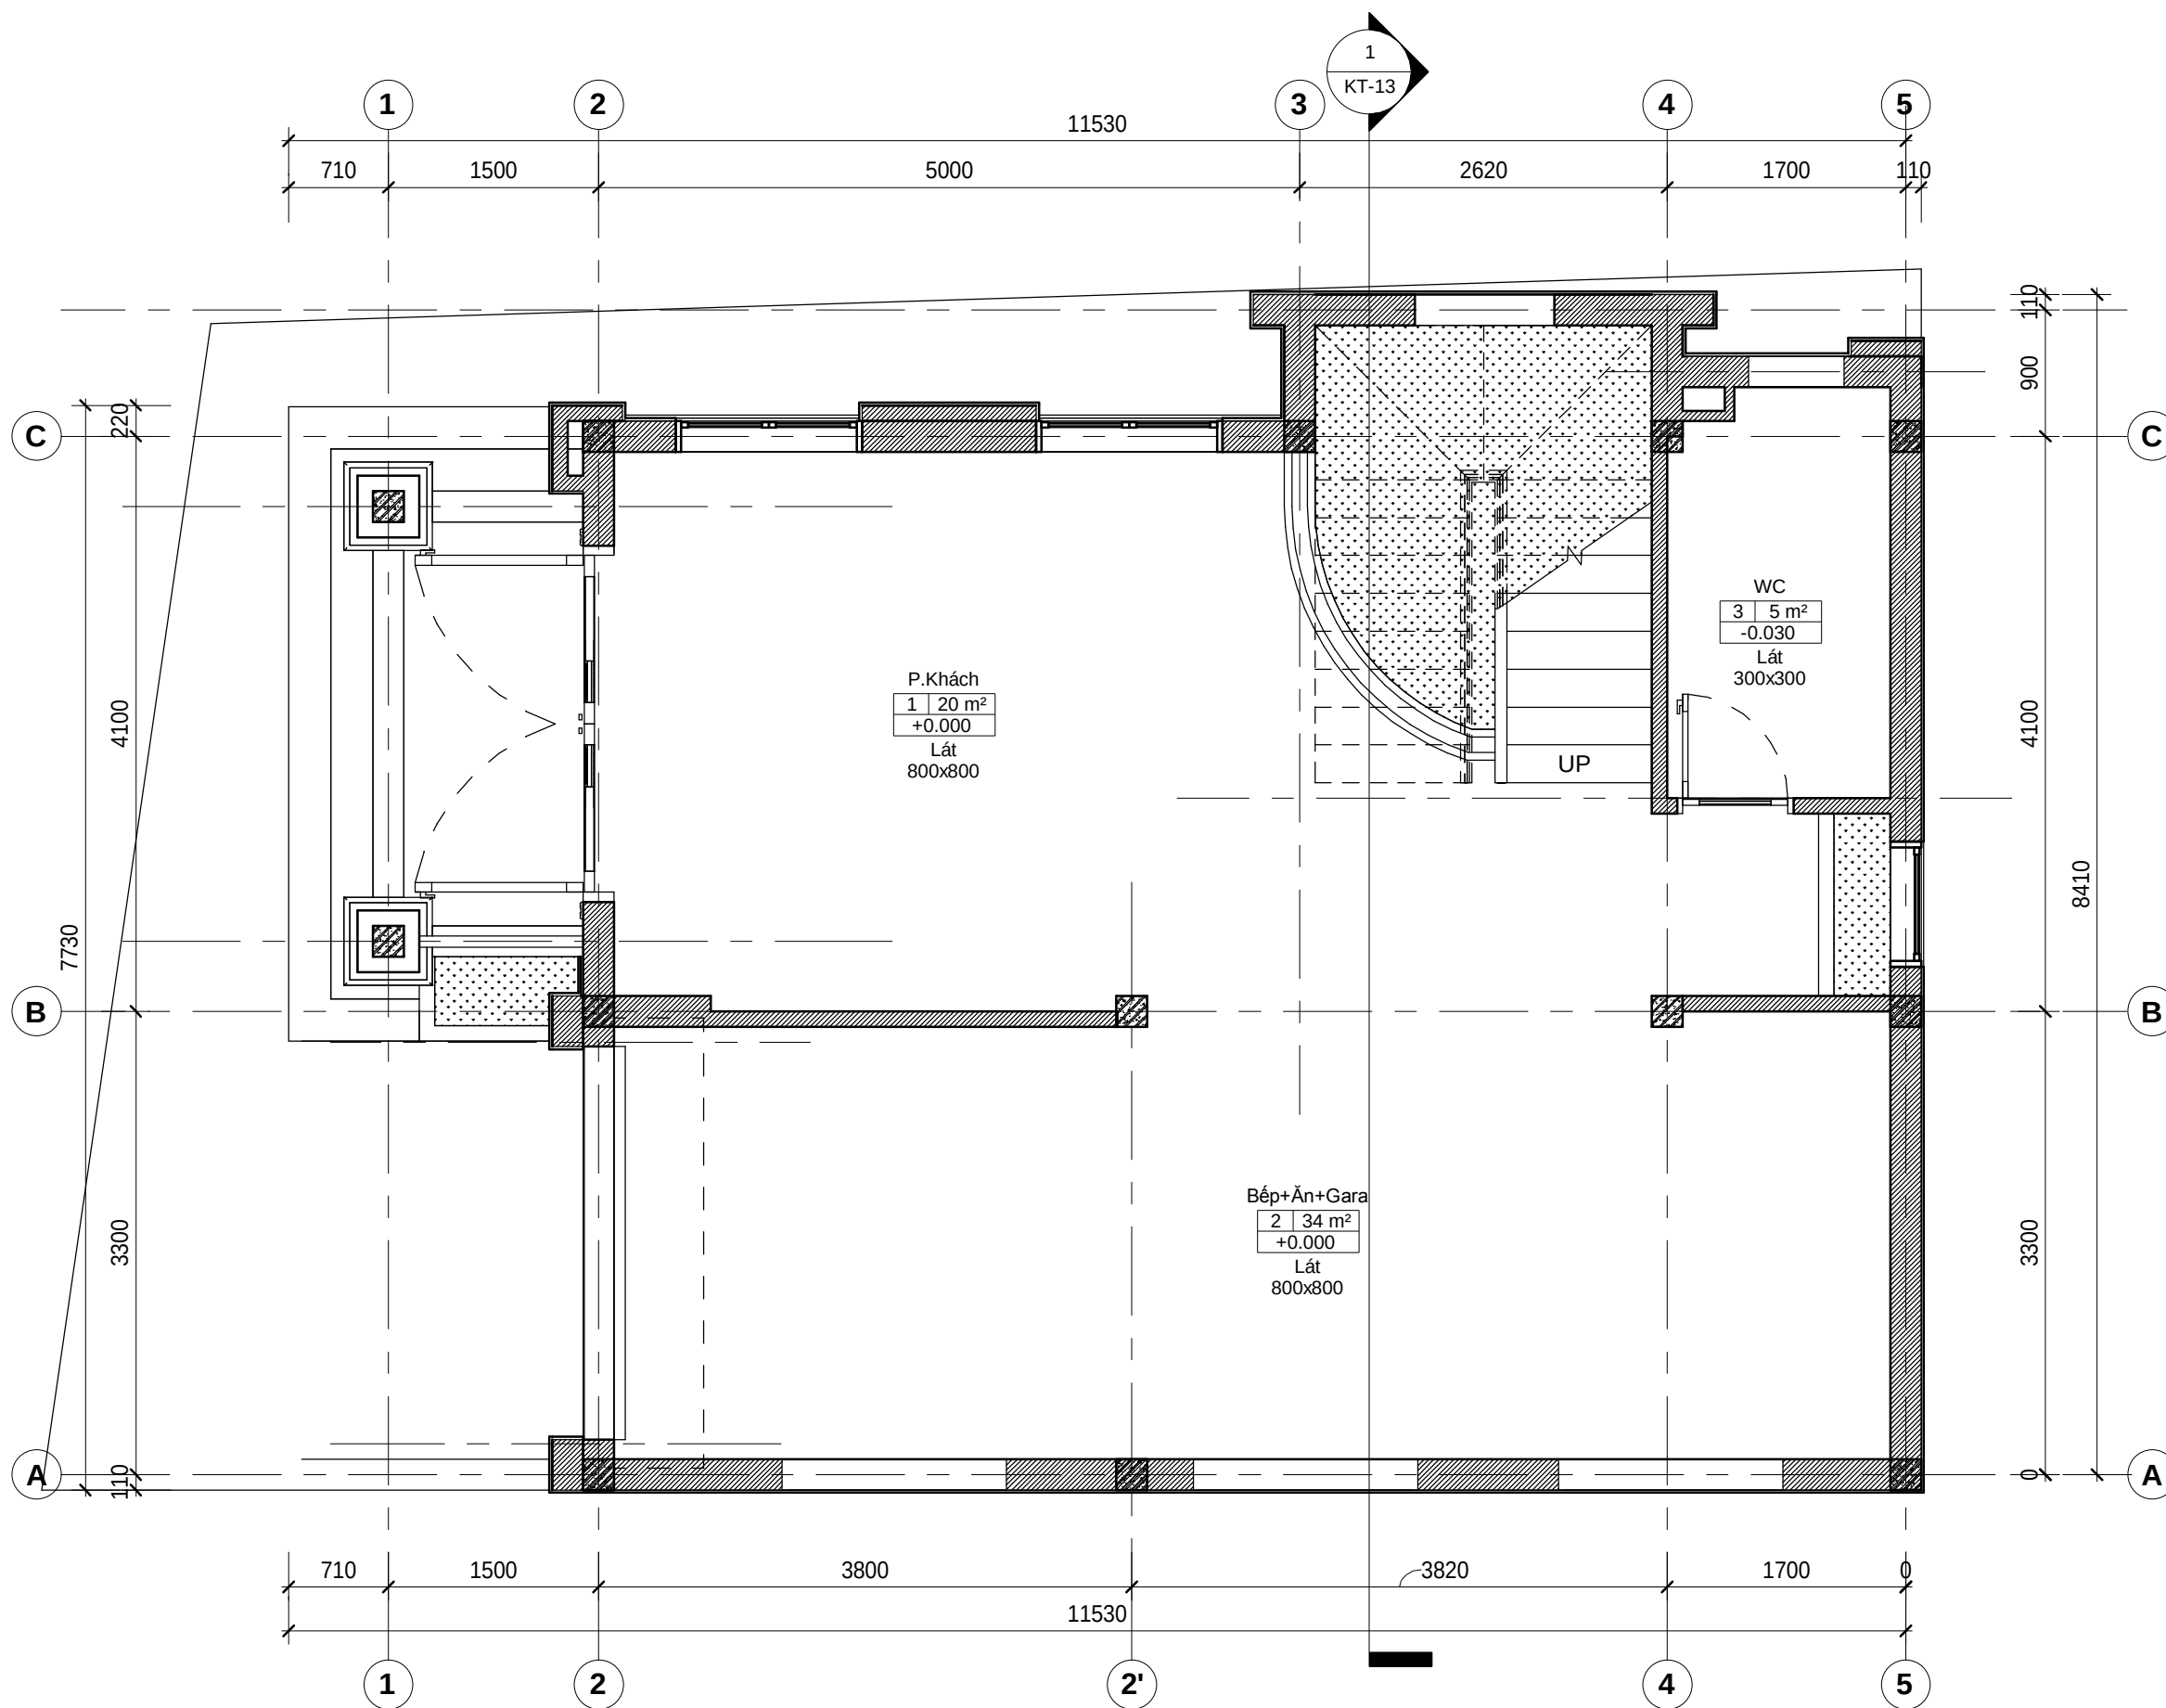

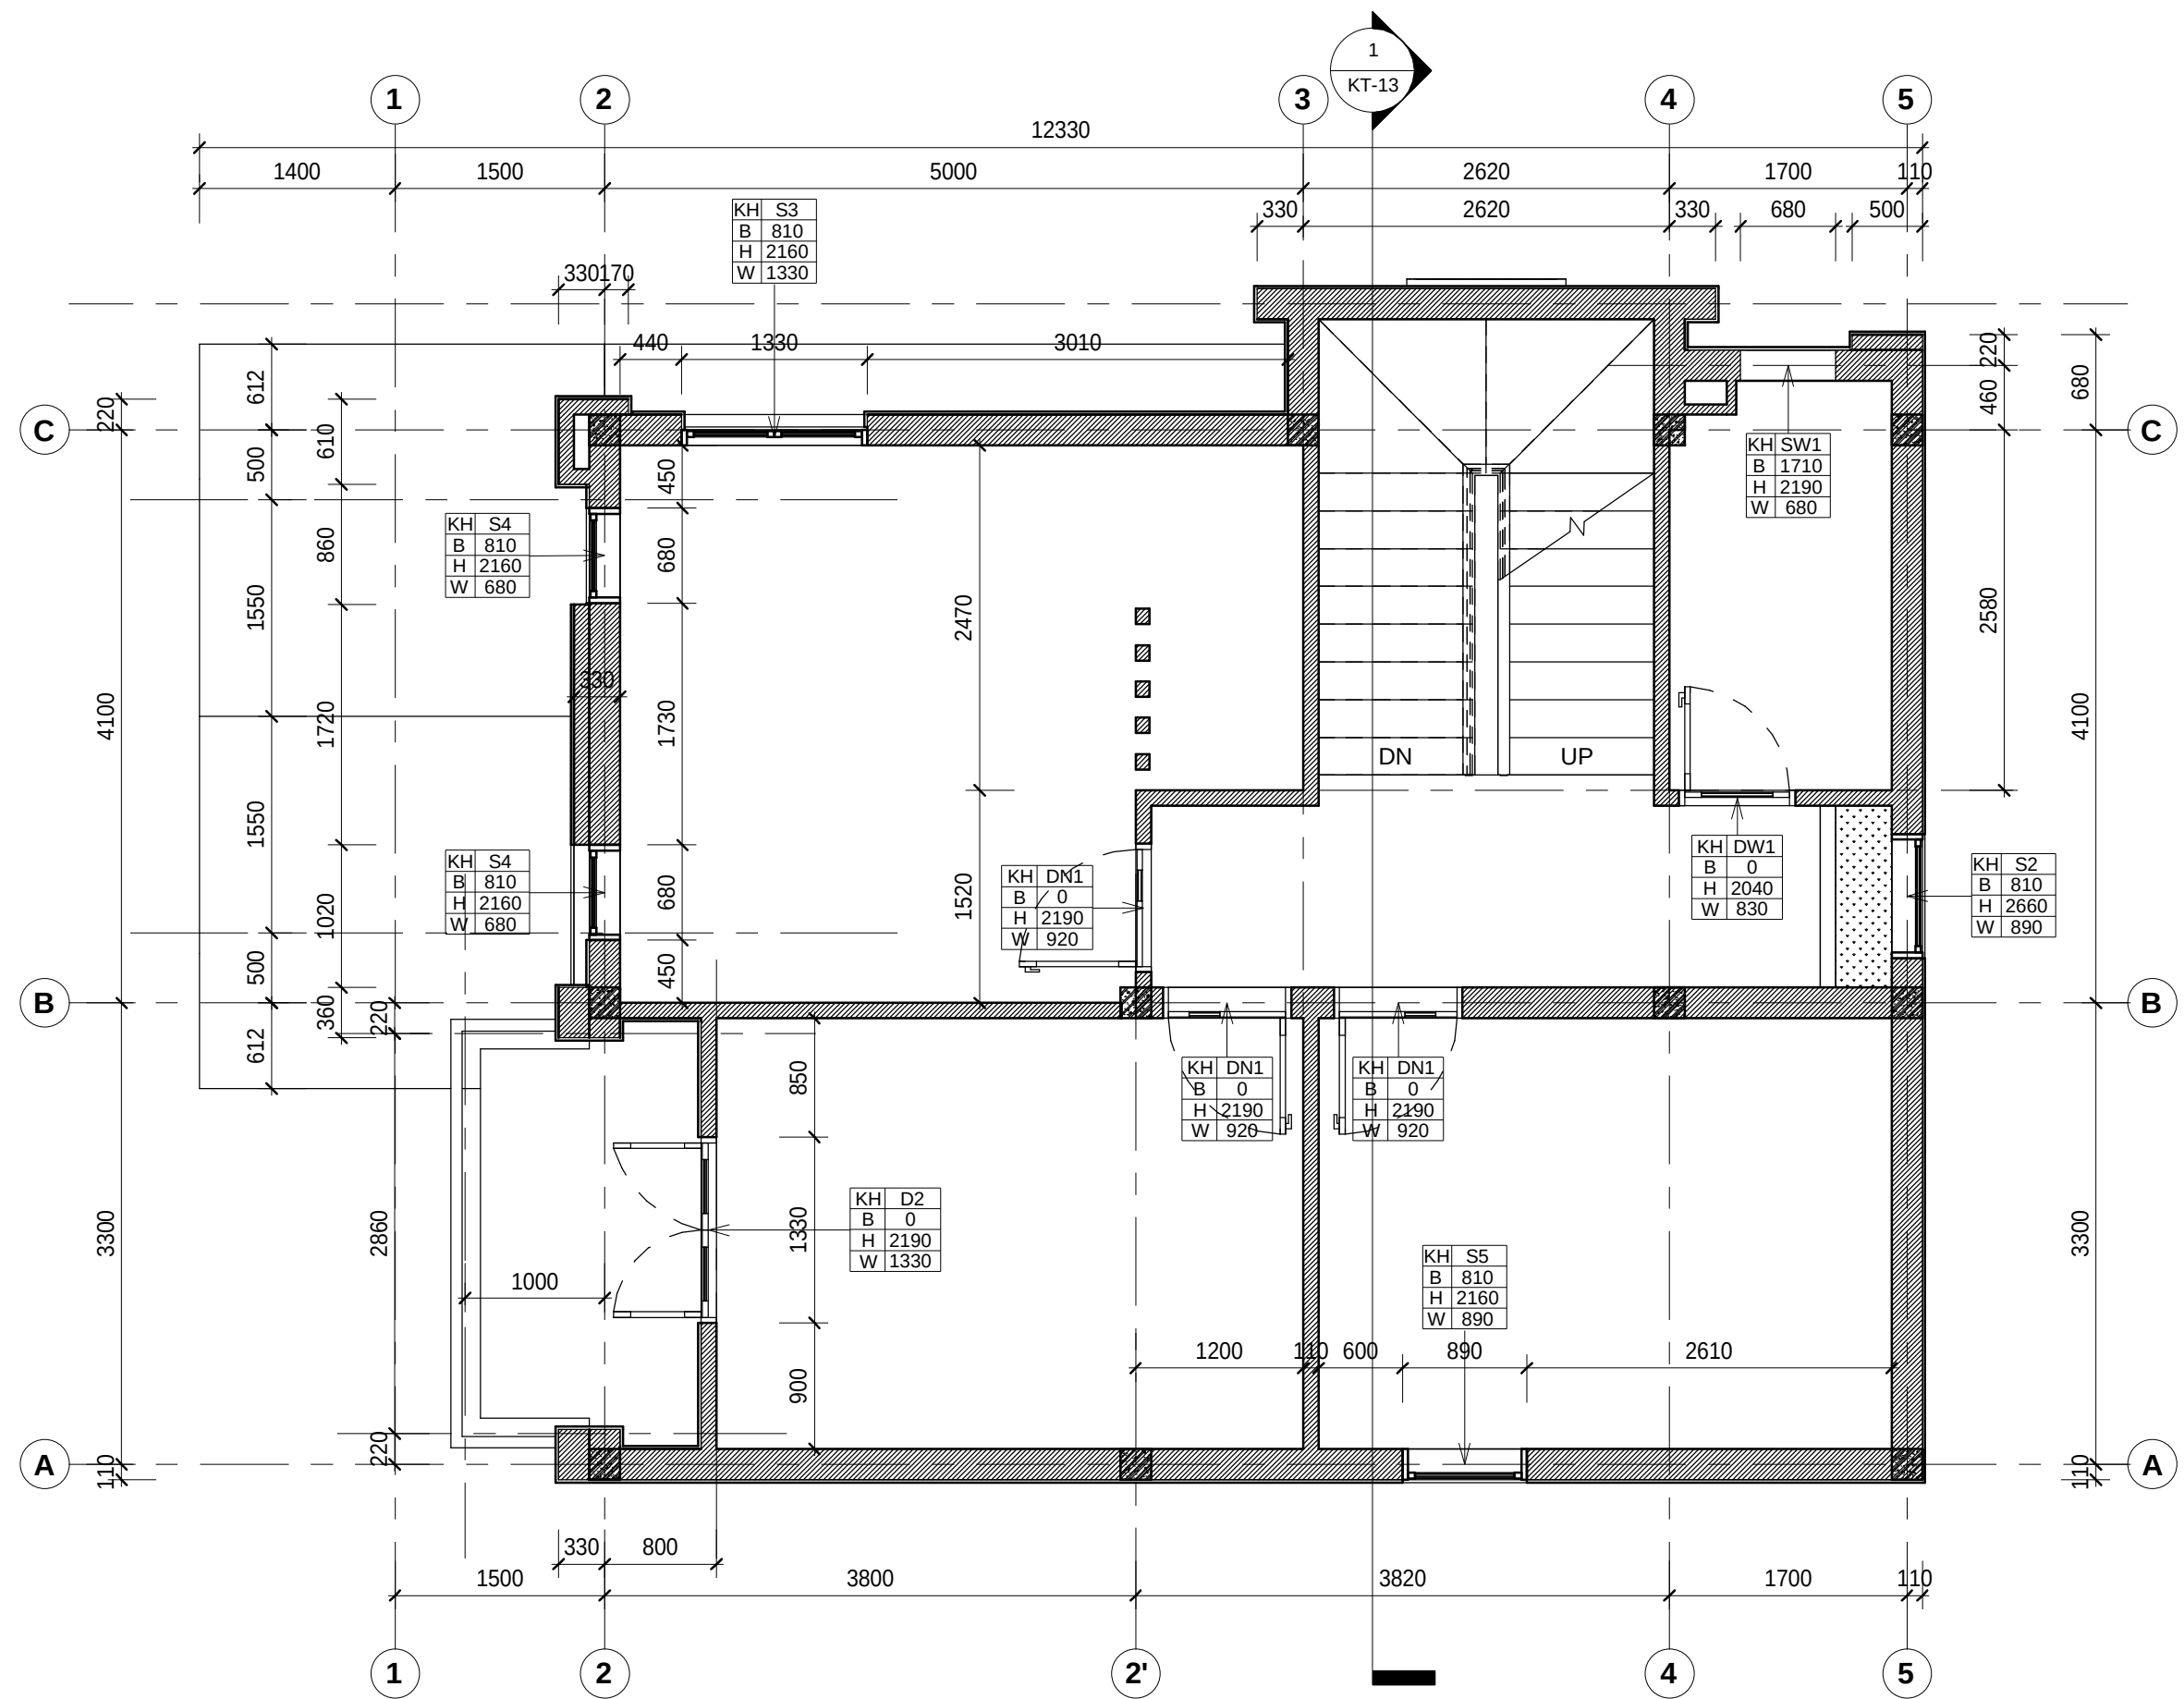


MẶT BẰNG BỐ TRÍ CỬA TẦNG 2

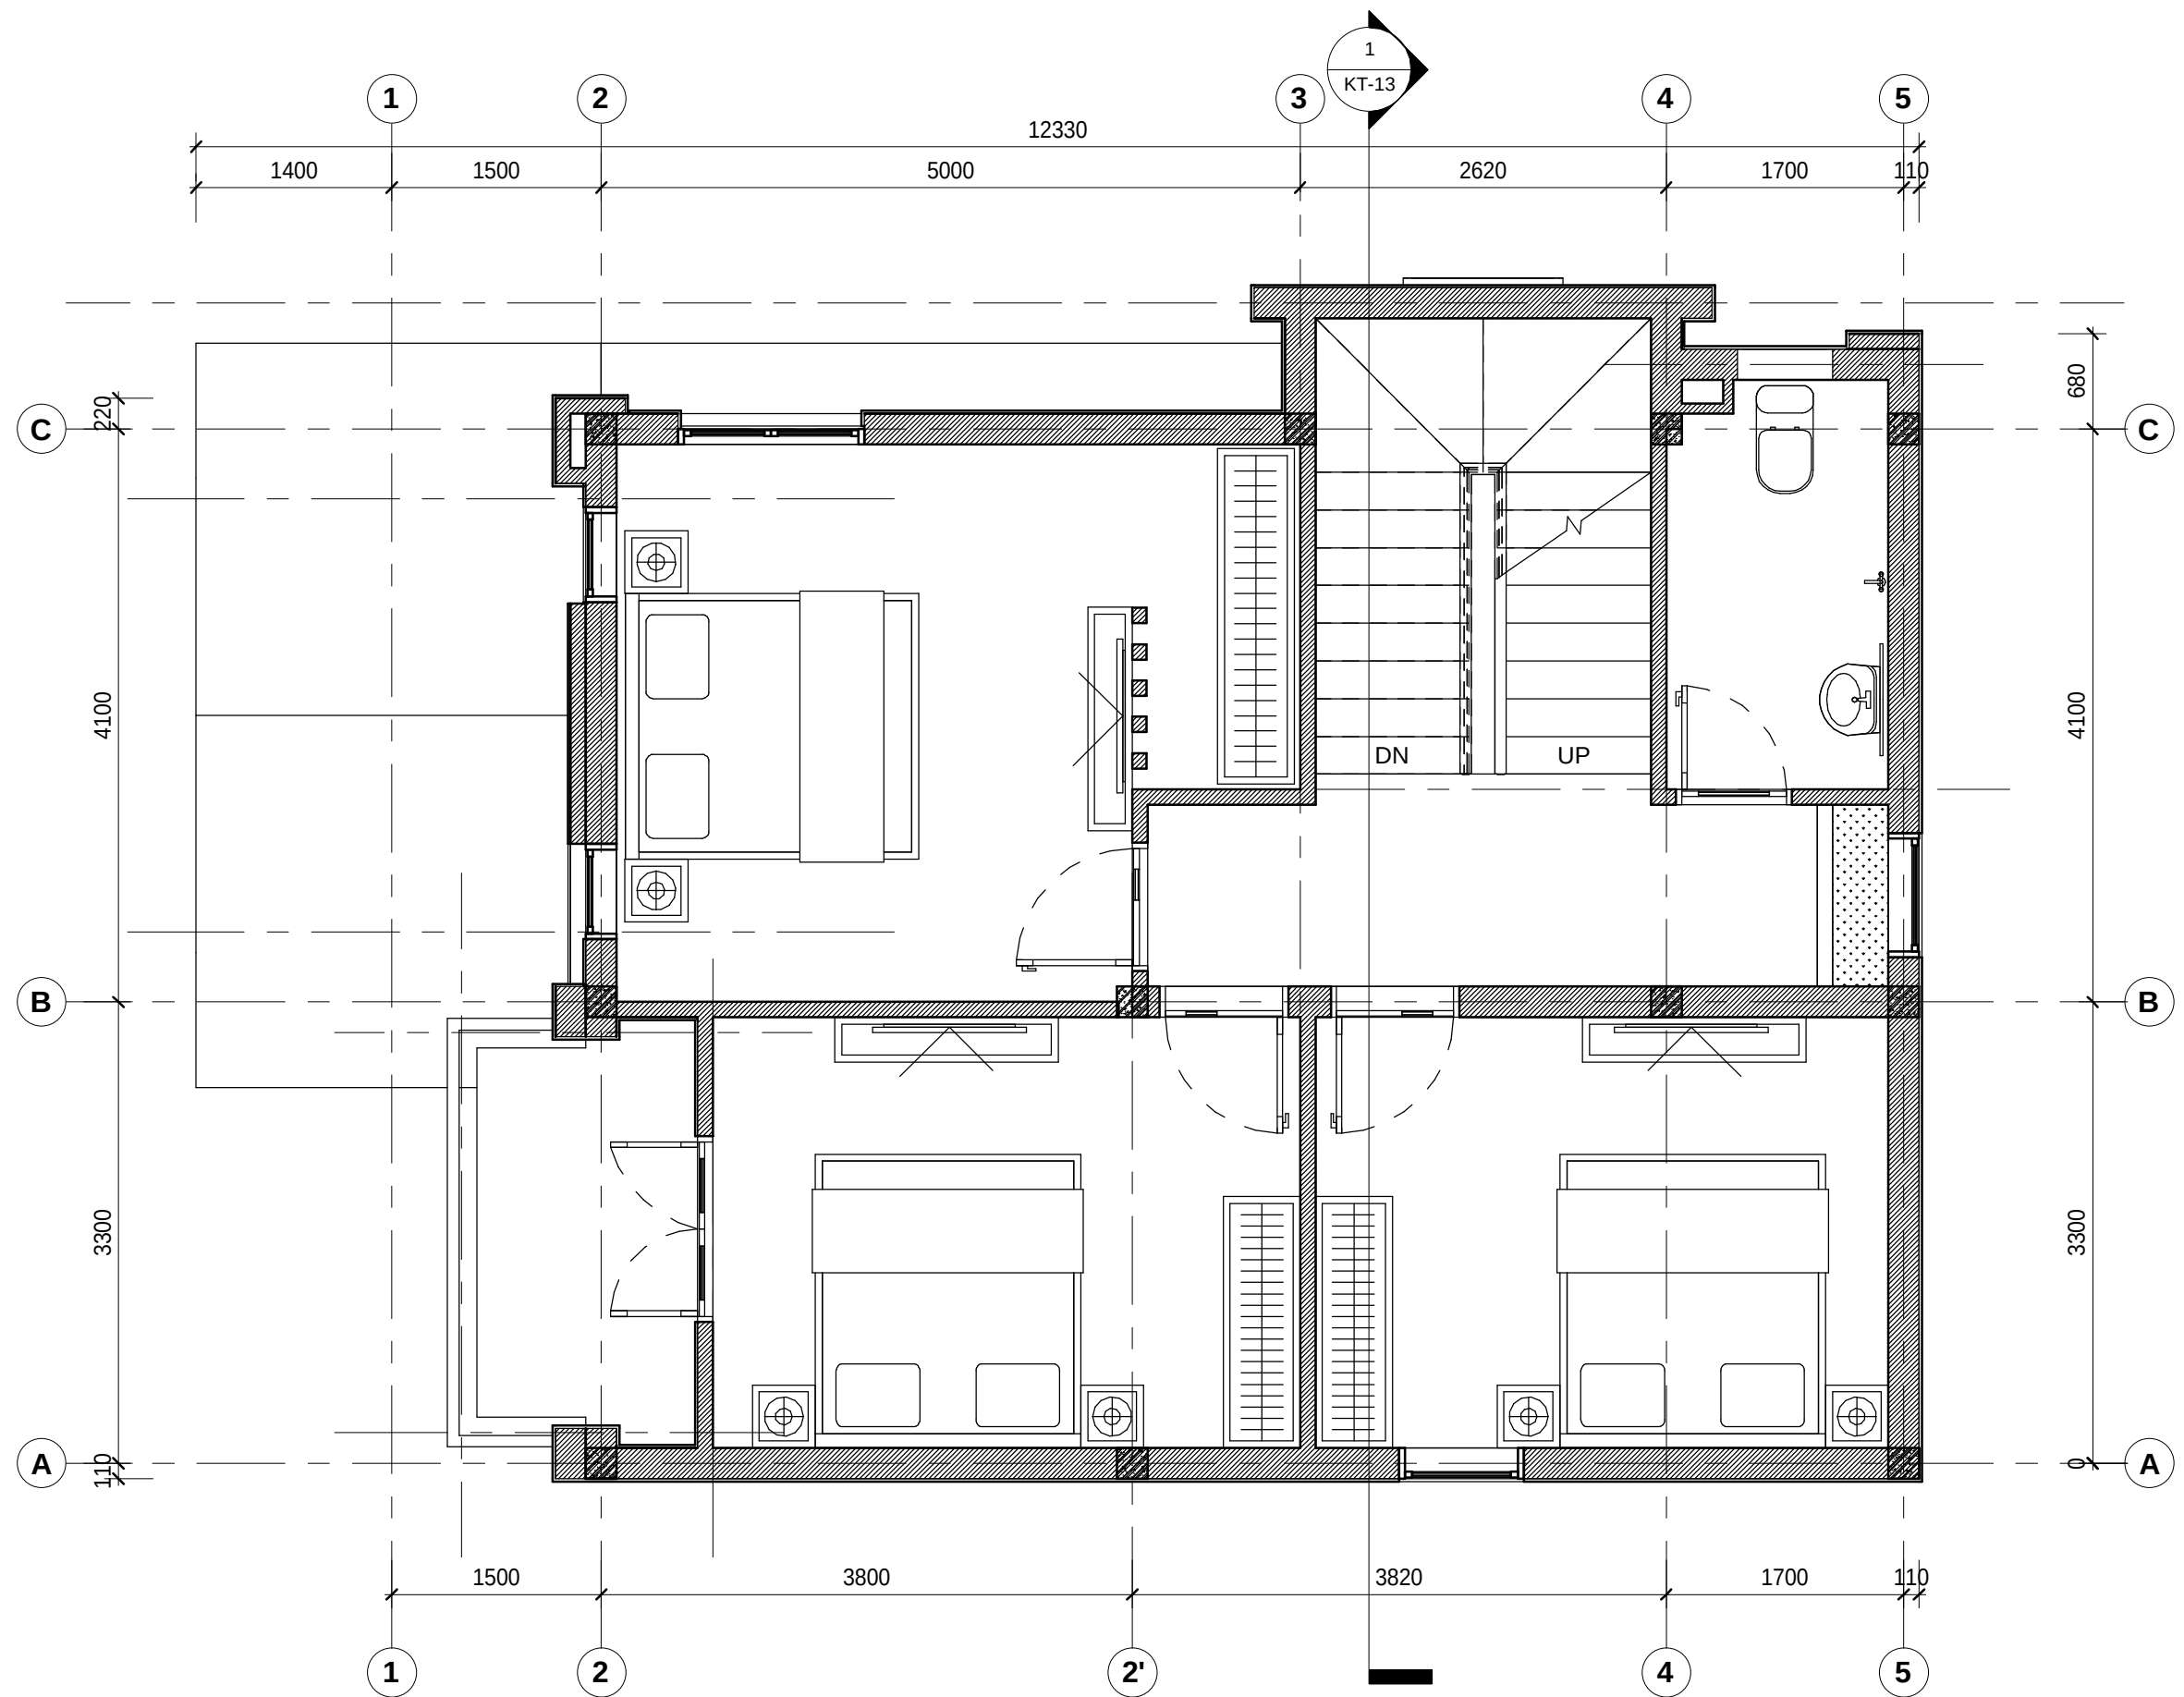


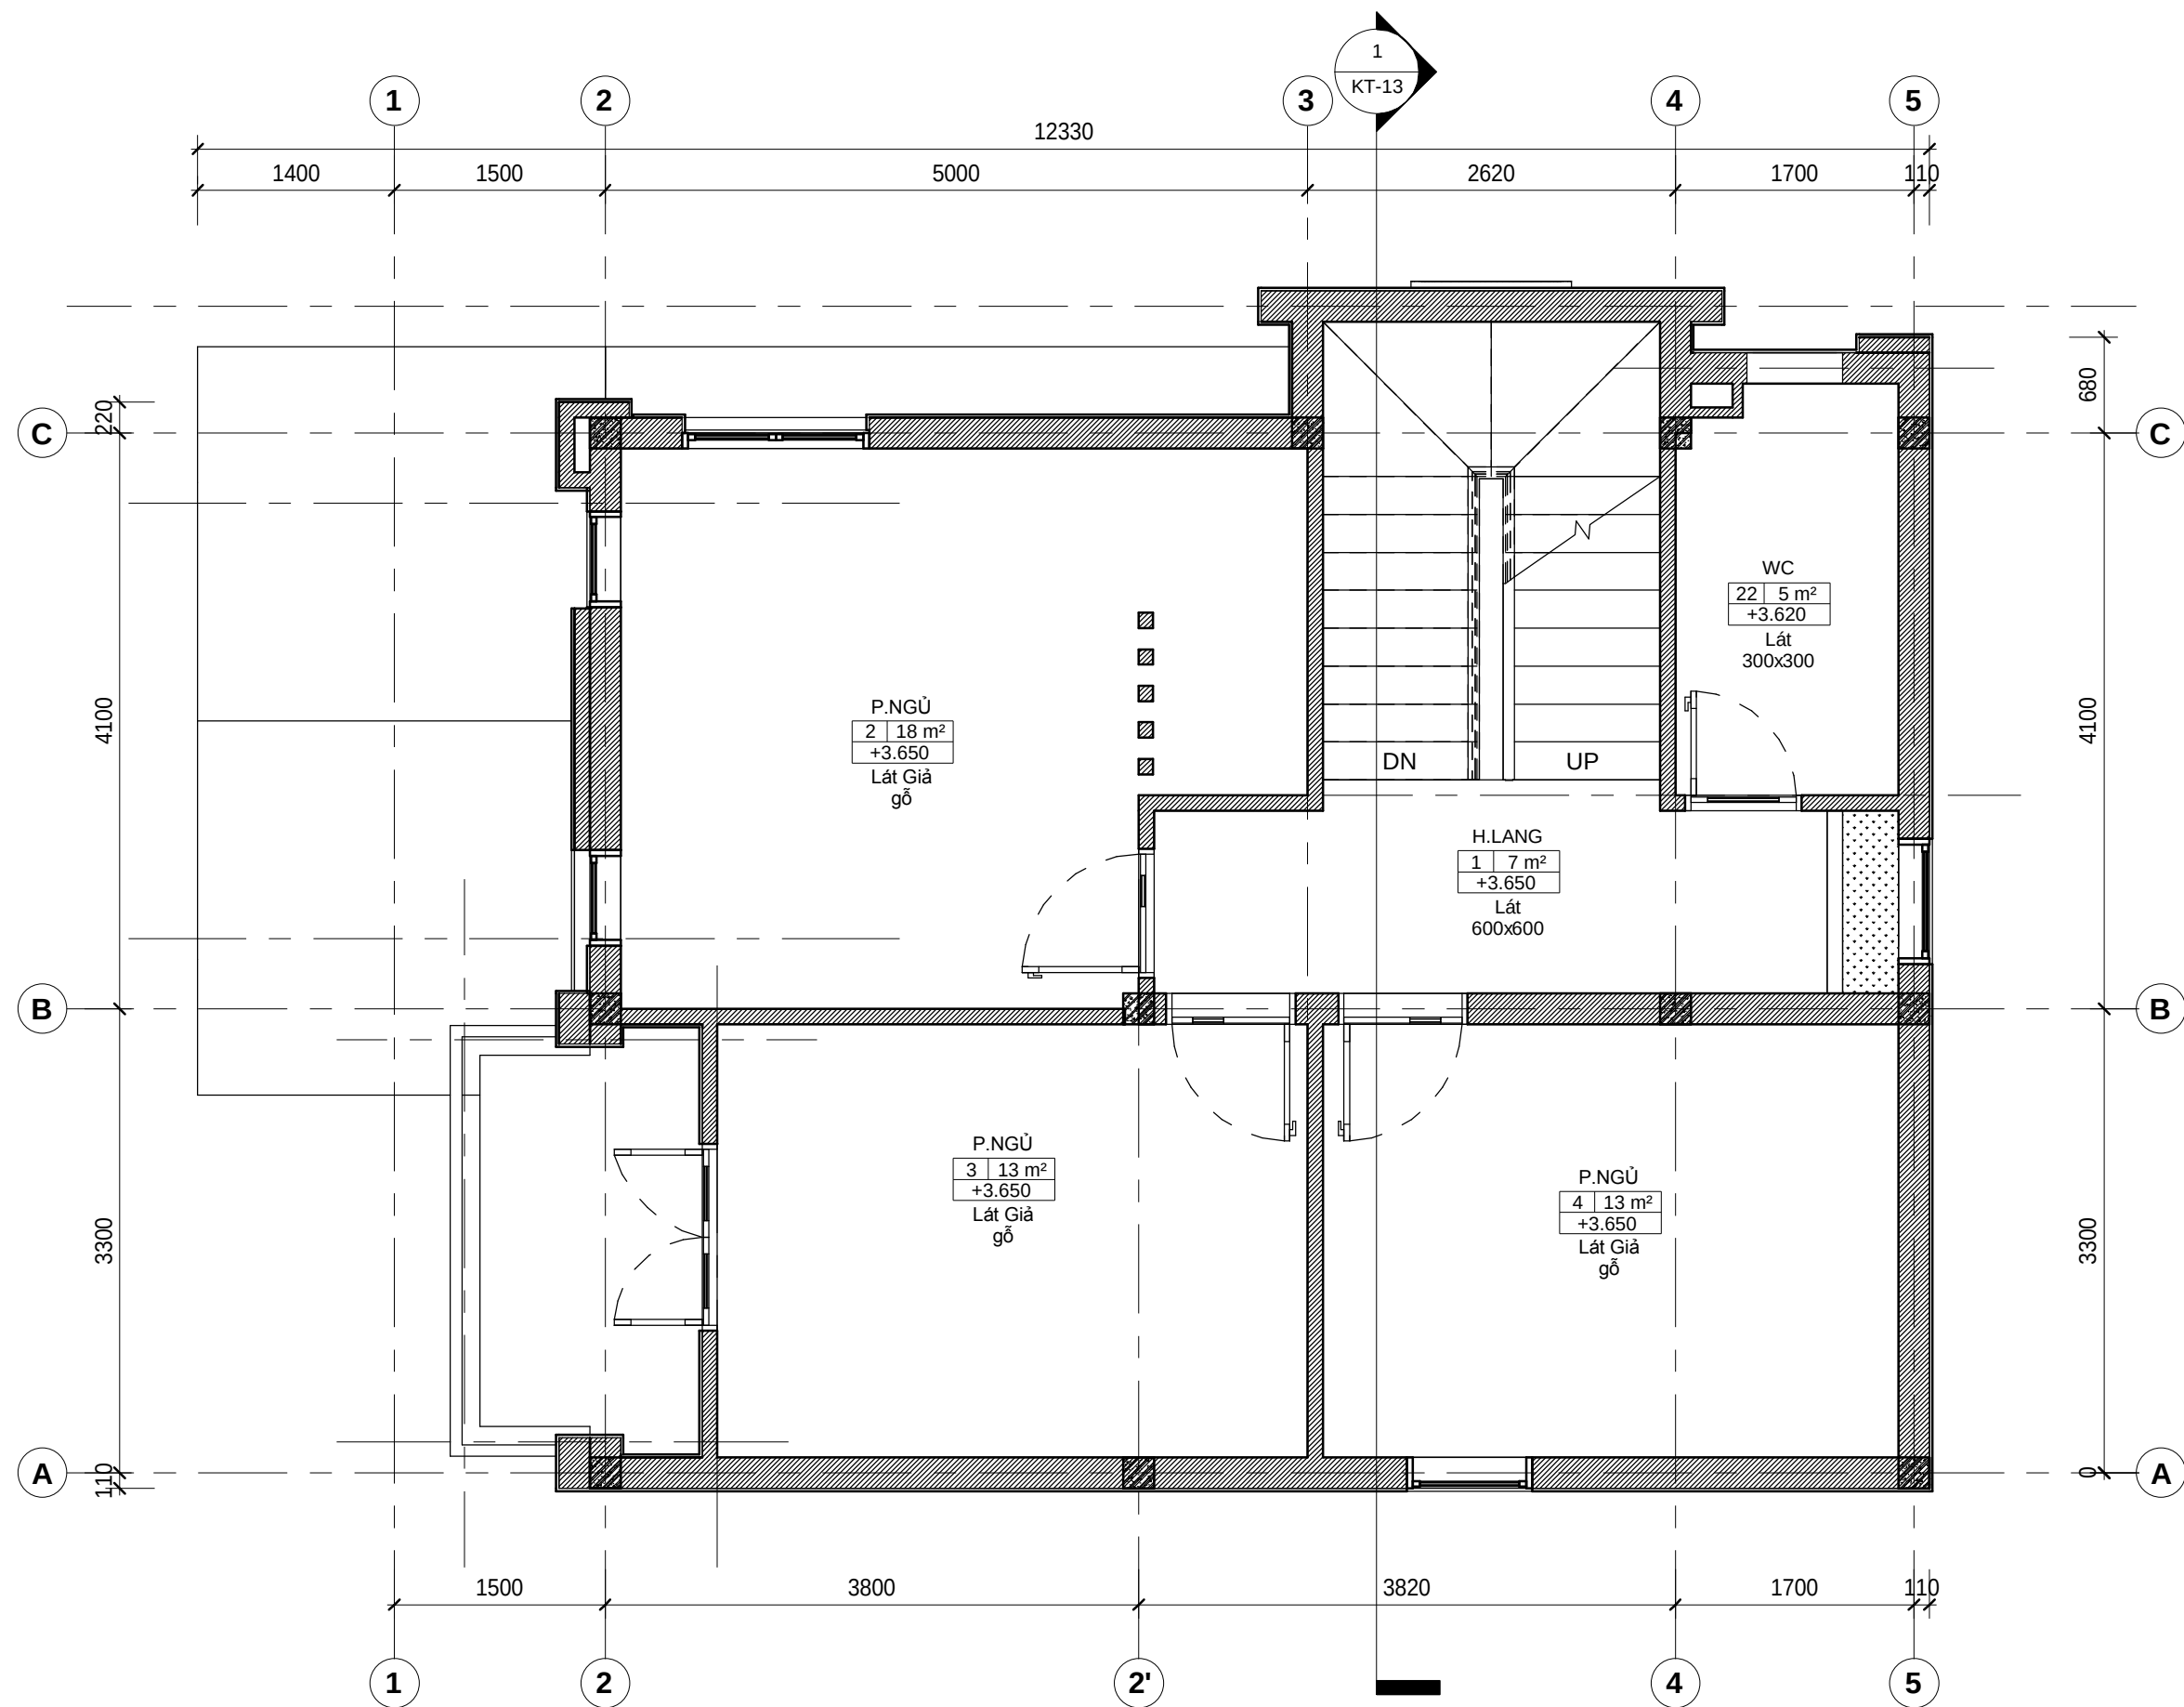


MẶT BẰNG SÀN TẦNG 2


KT-06

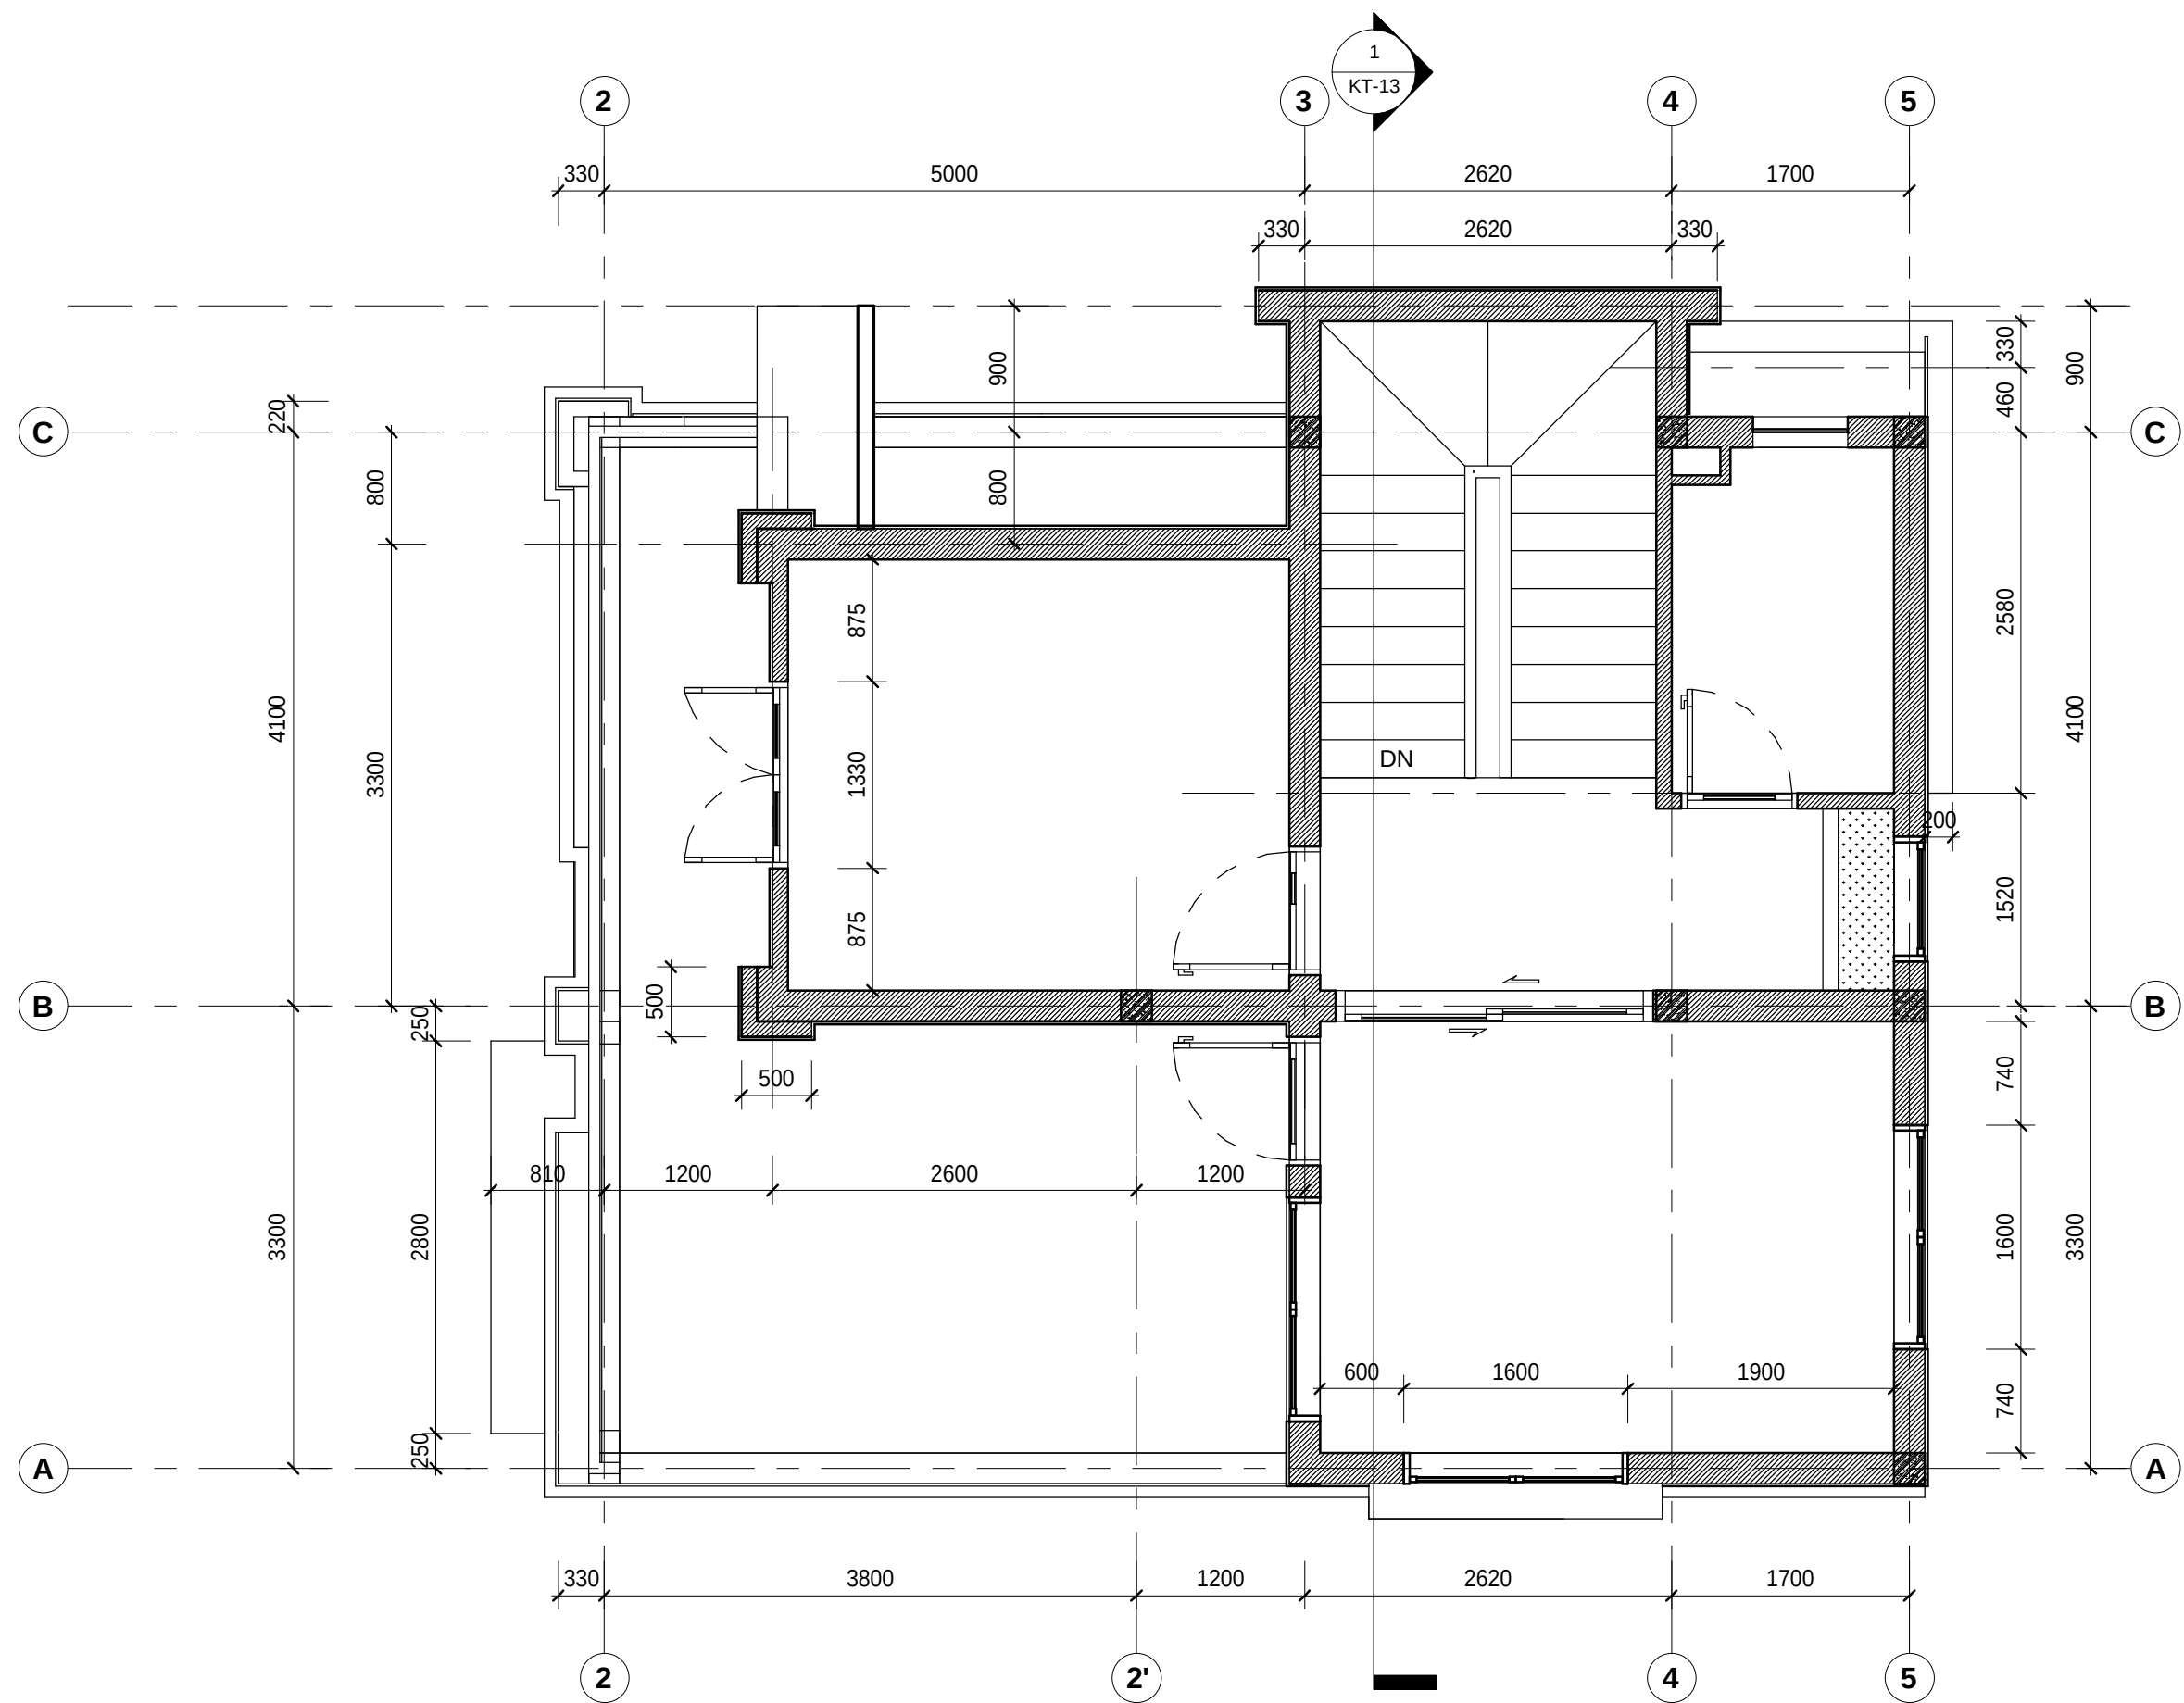

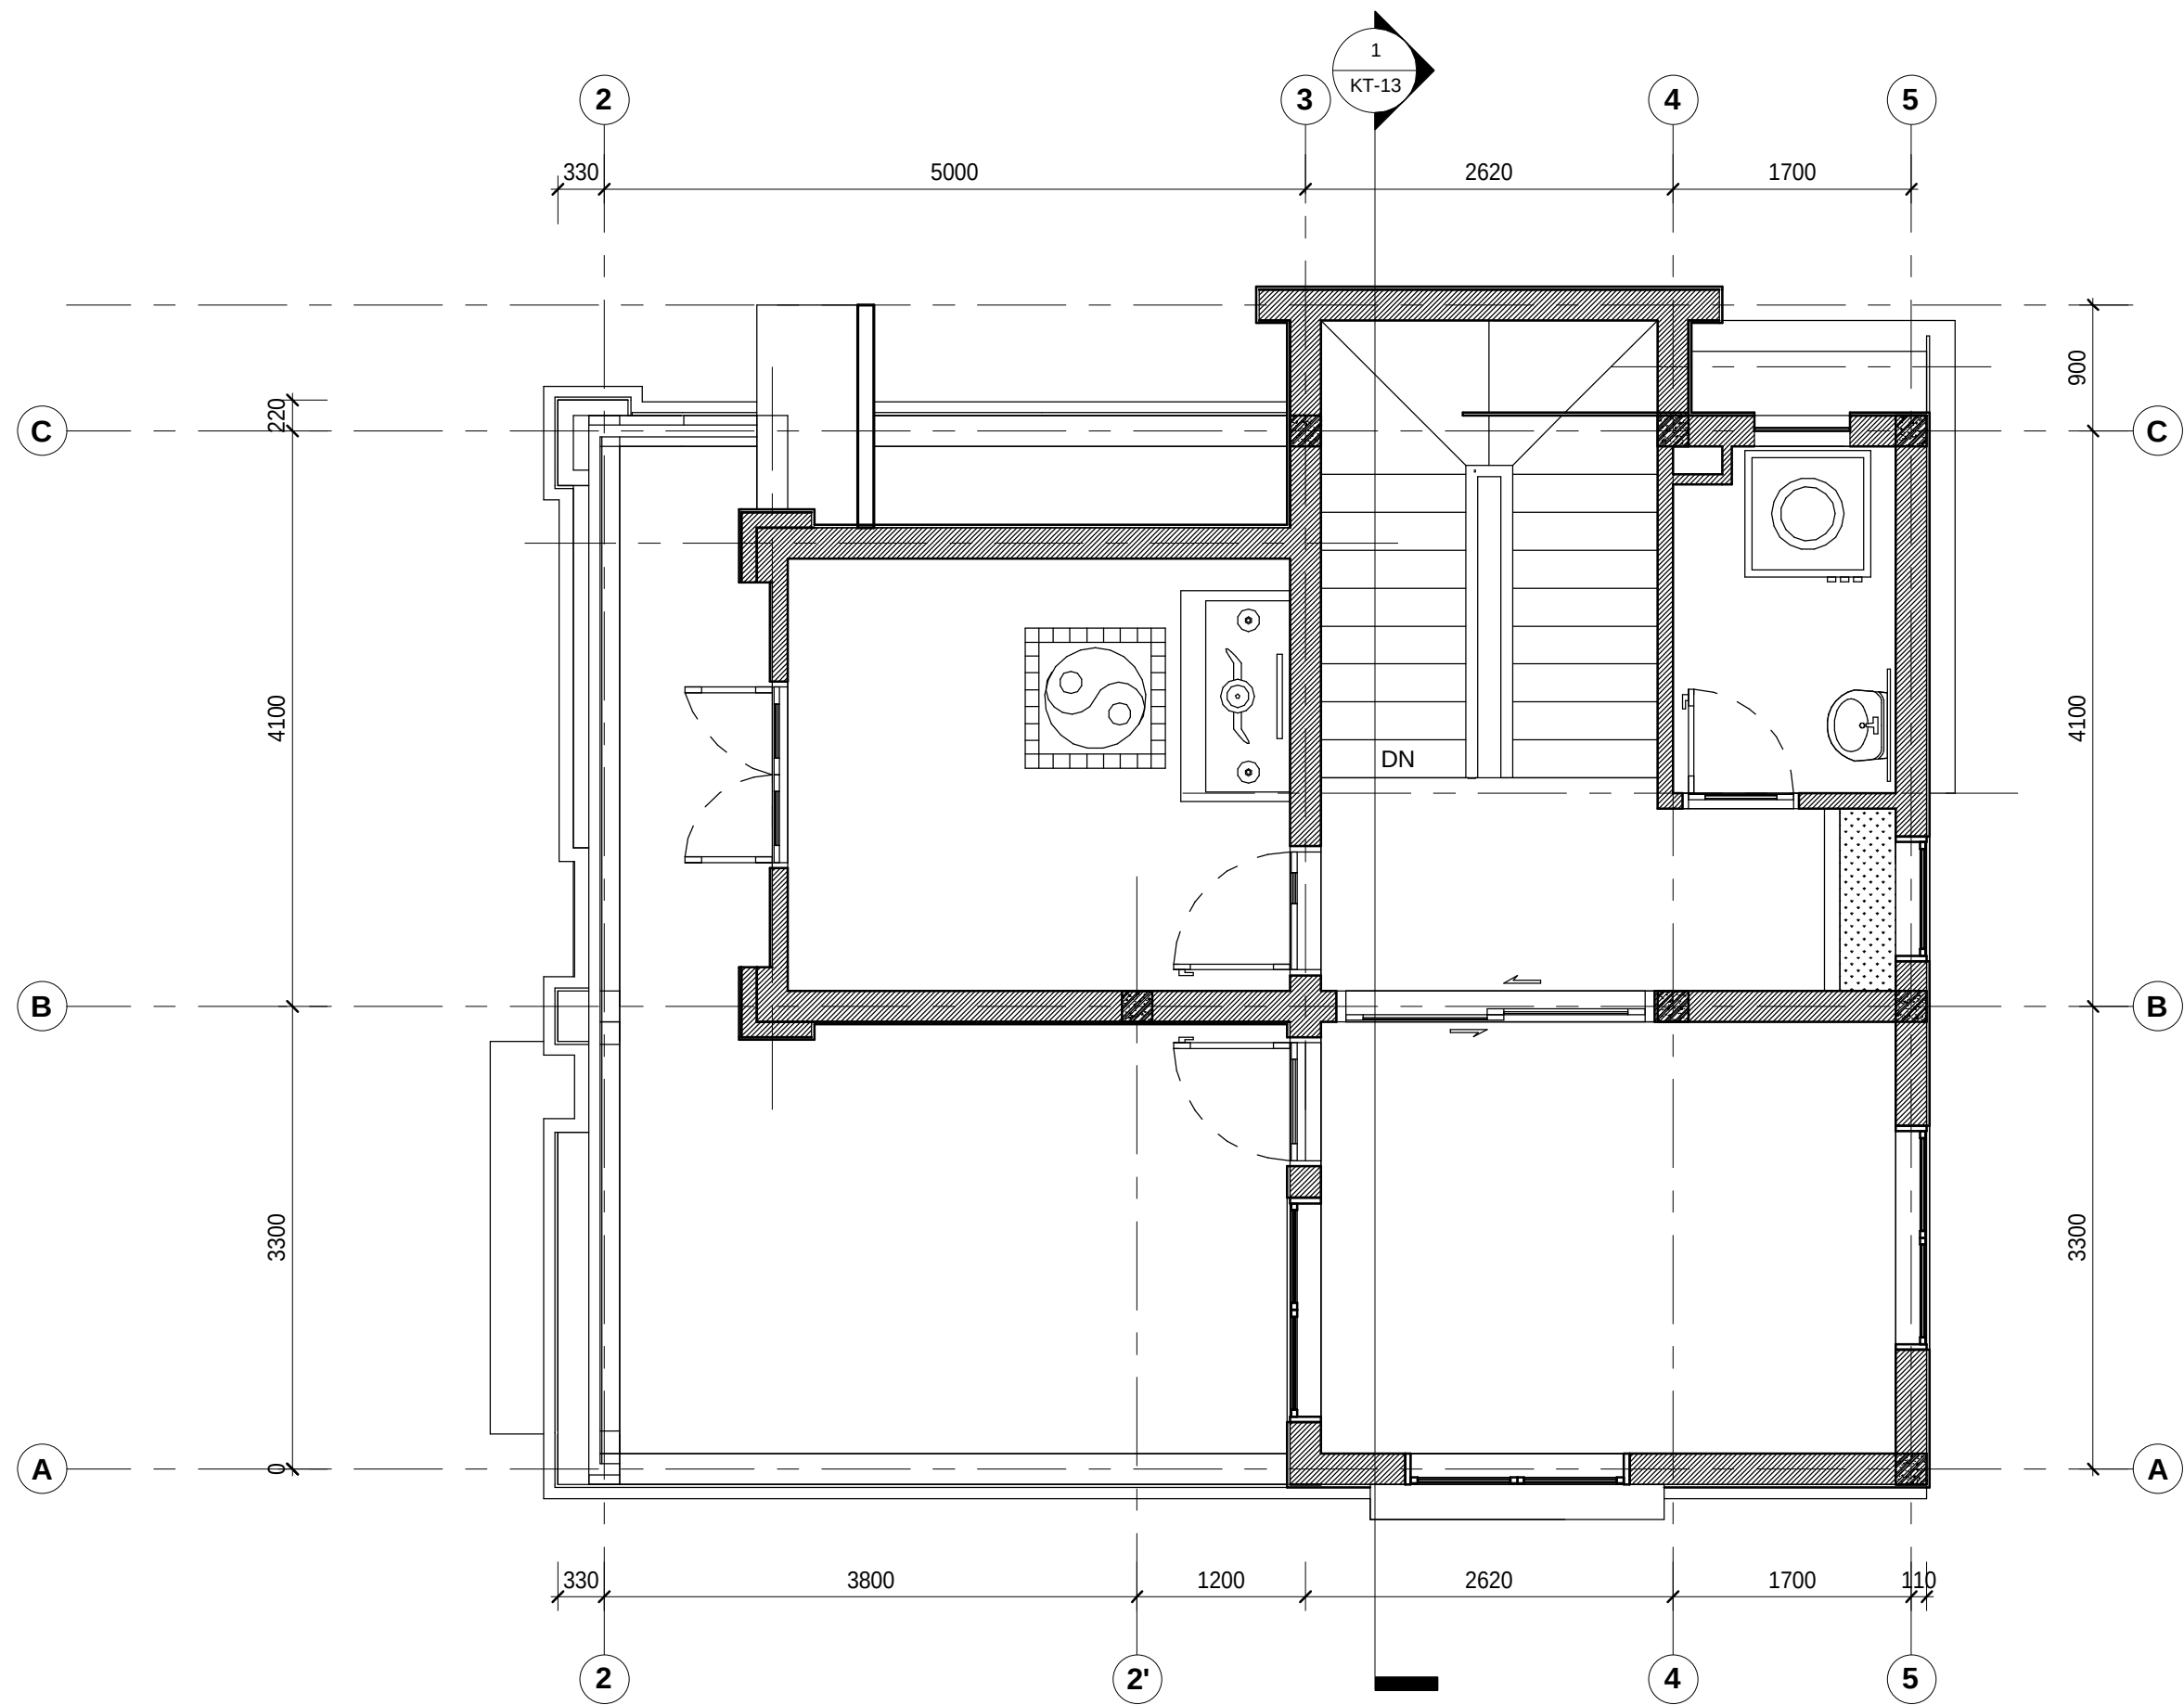

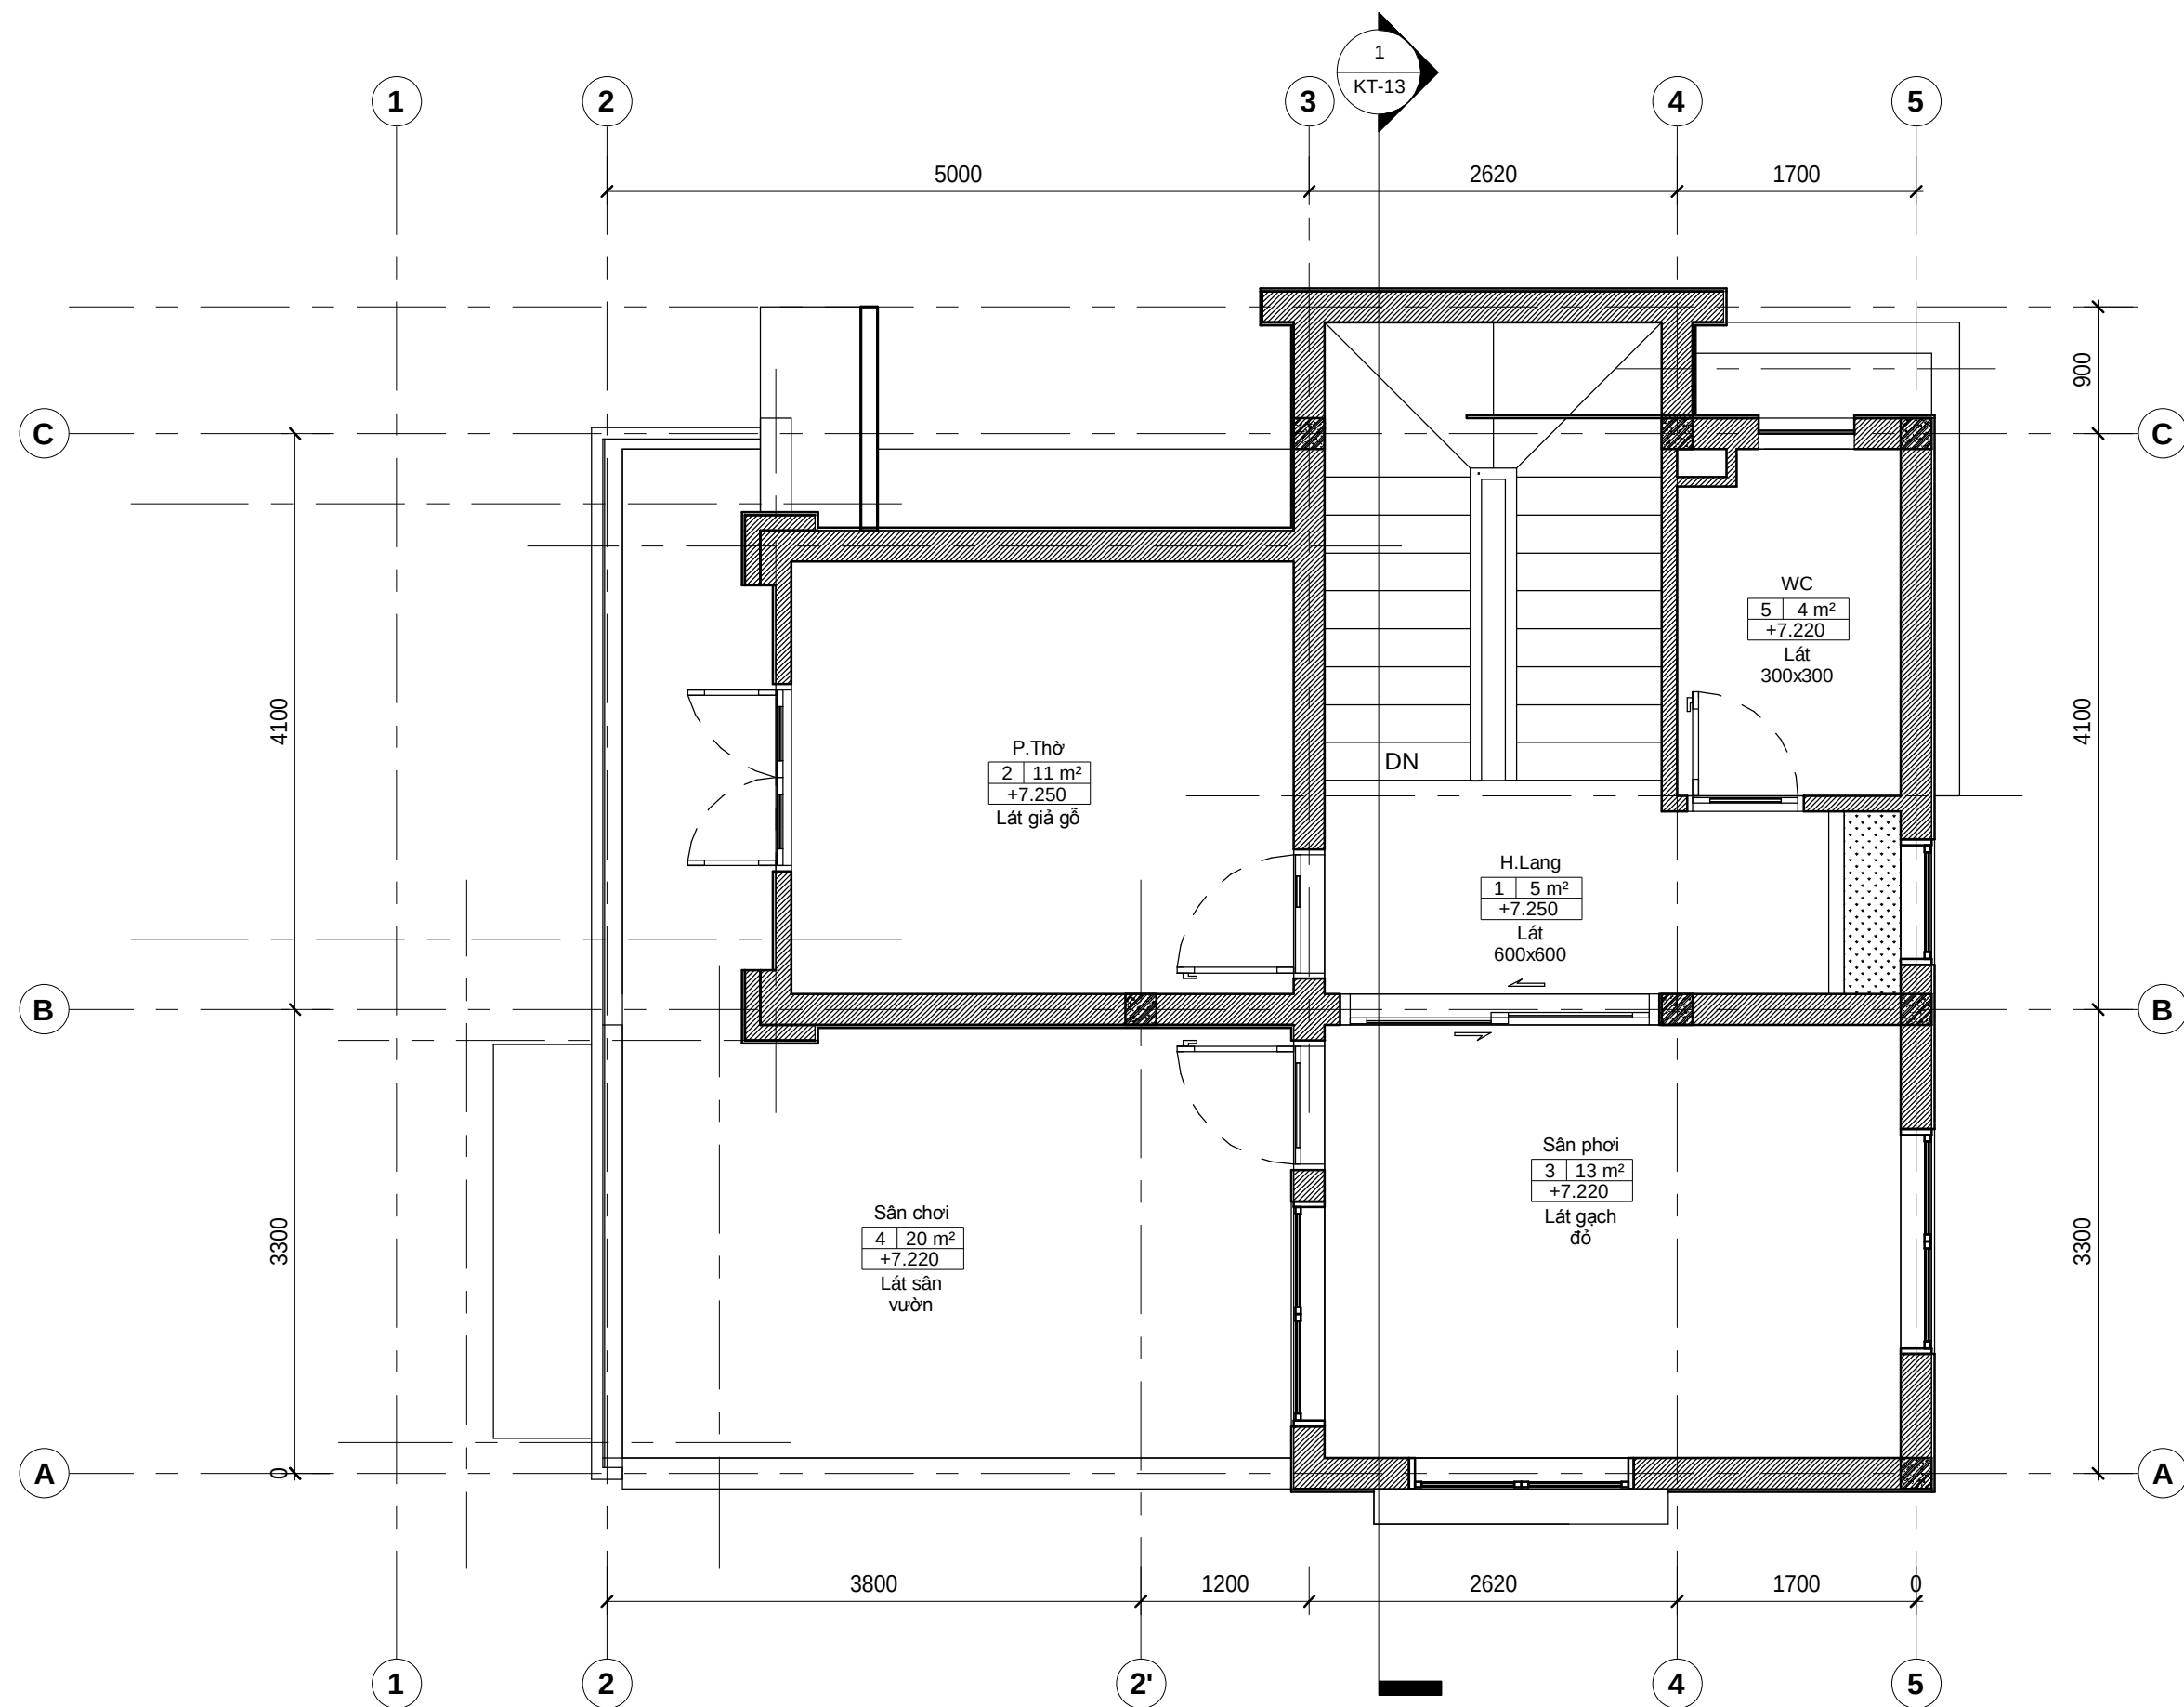



MẶT BẰNG SÀN TẦNG 3

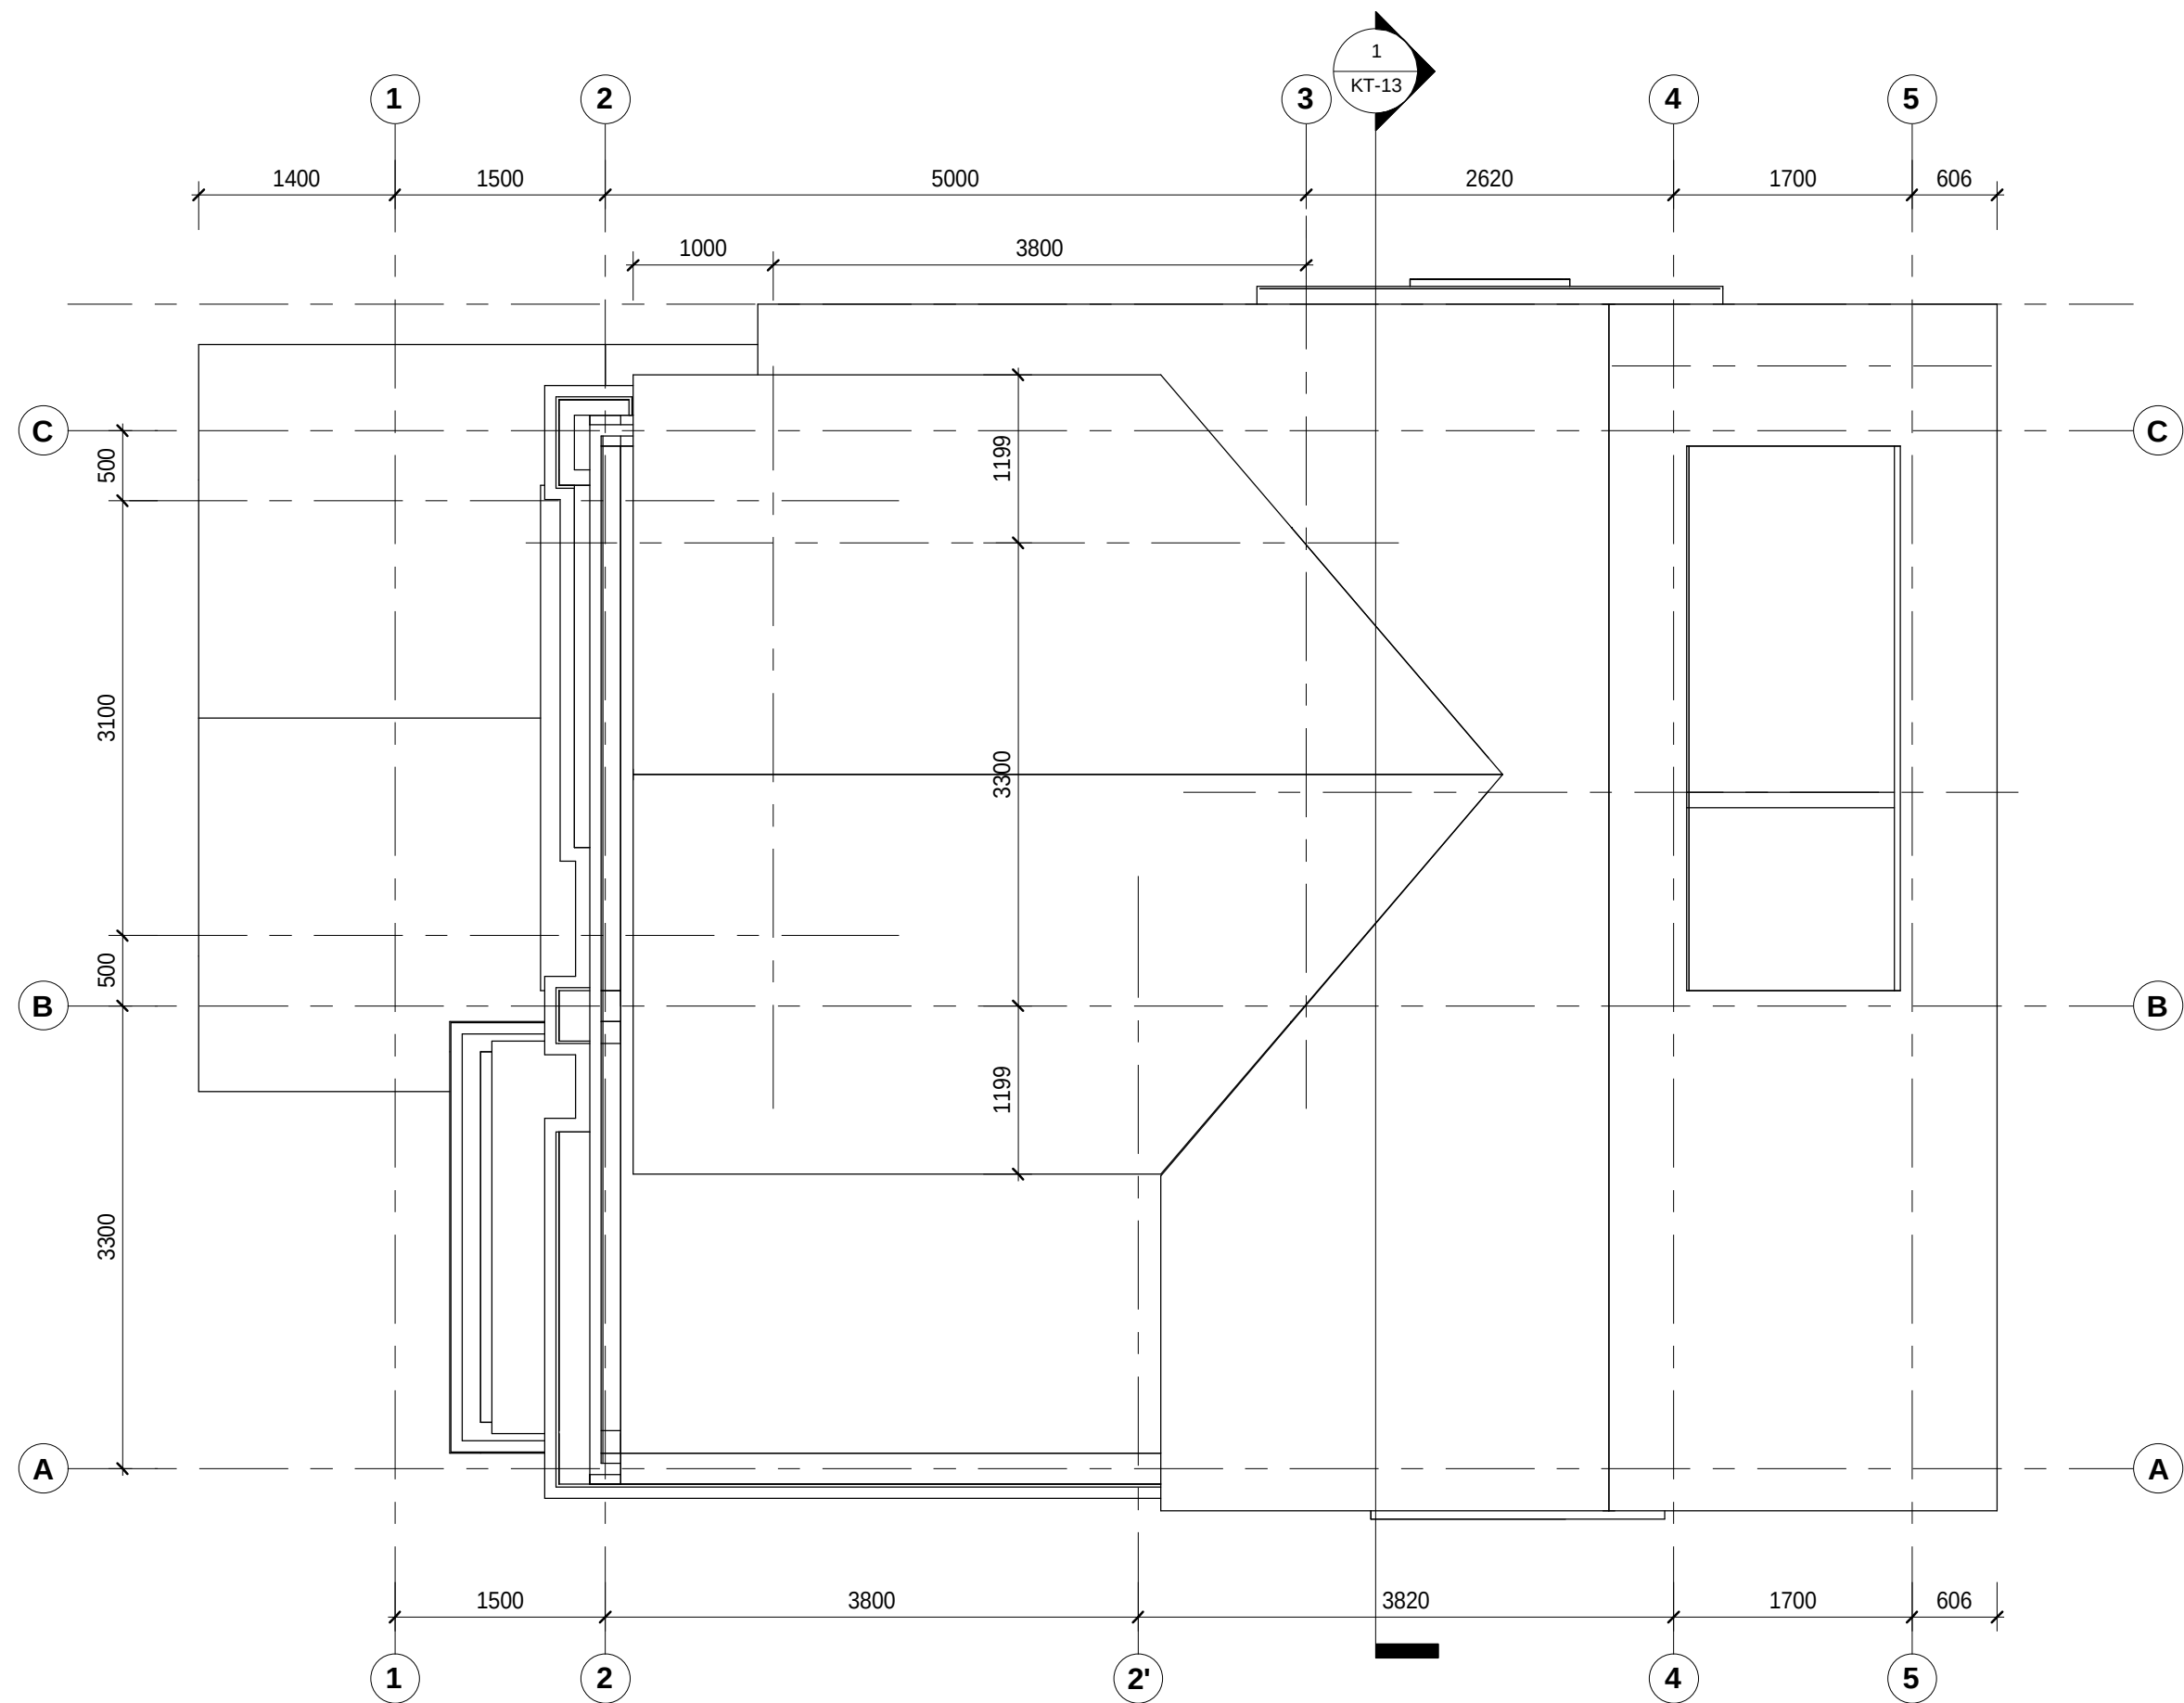


MẶT BẰNG MÁI

KT-10

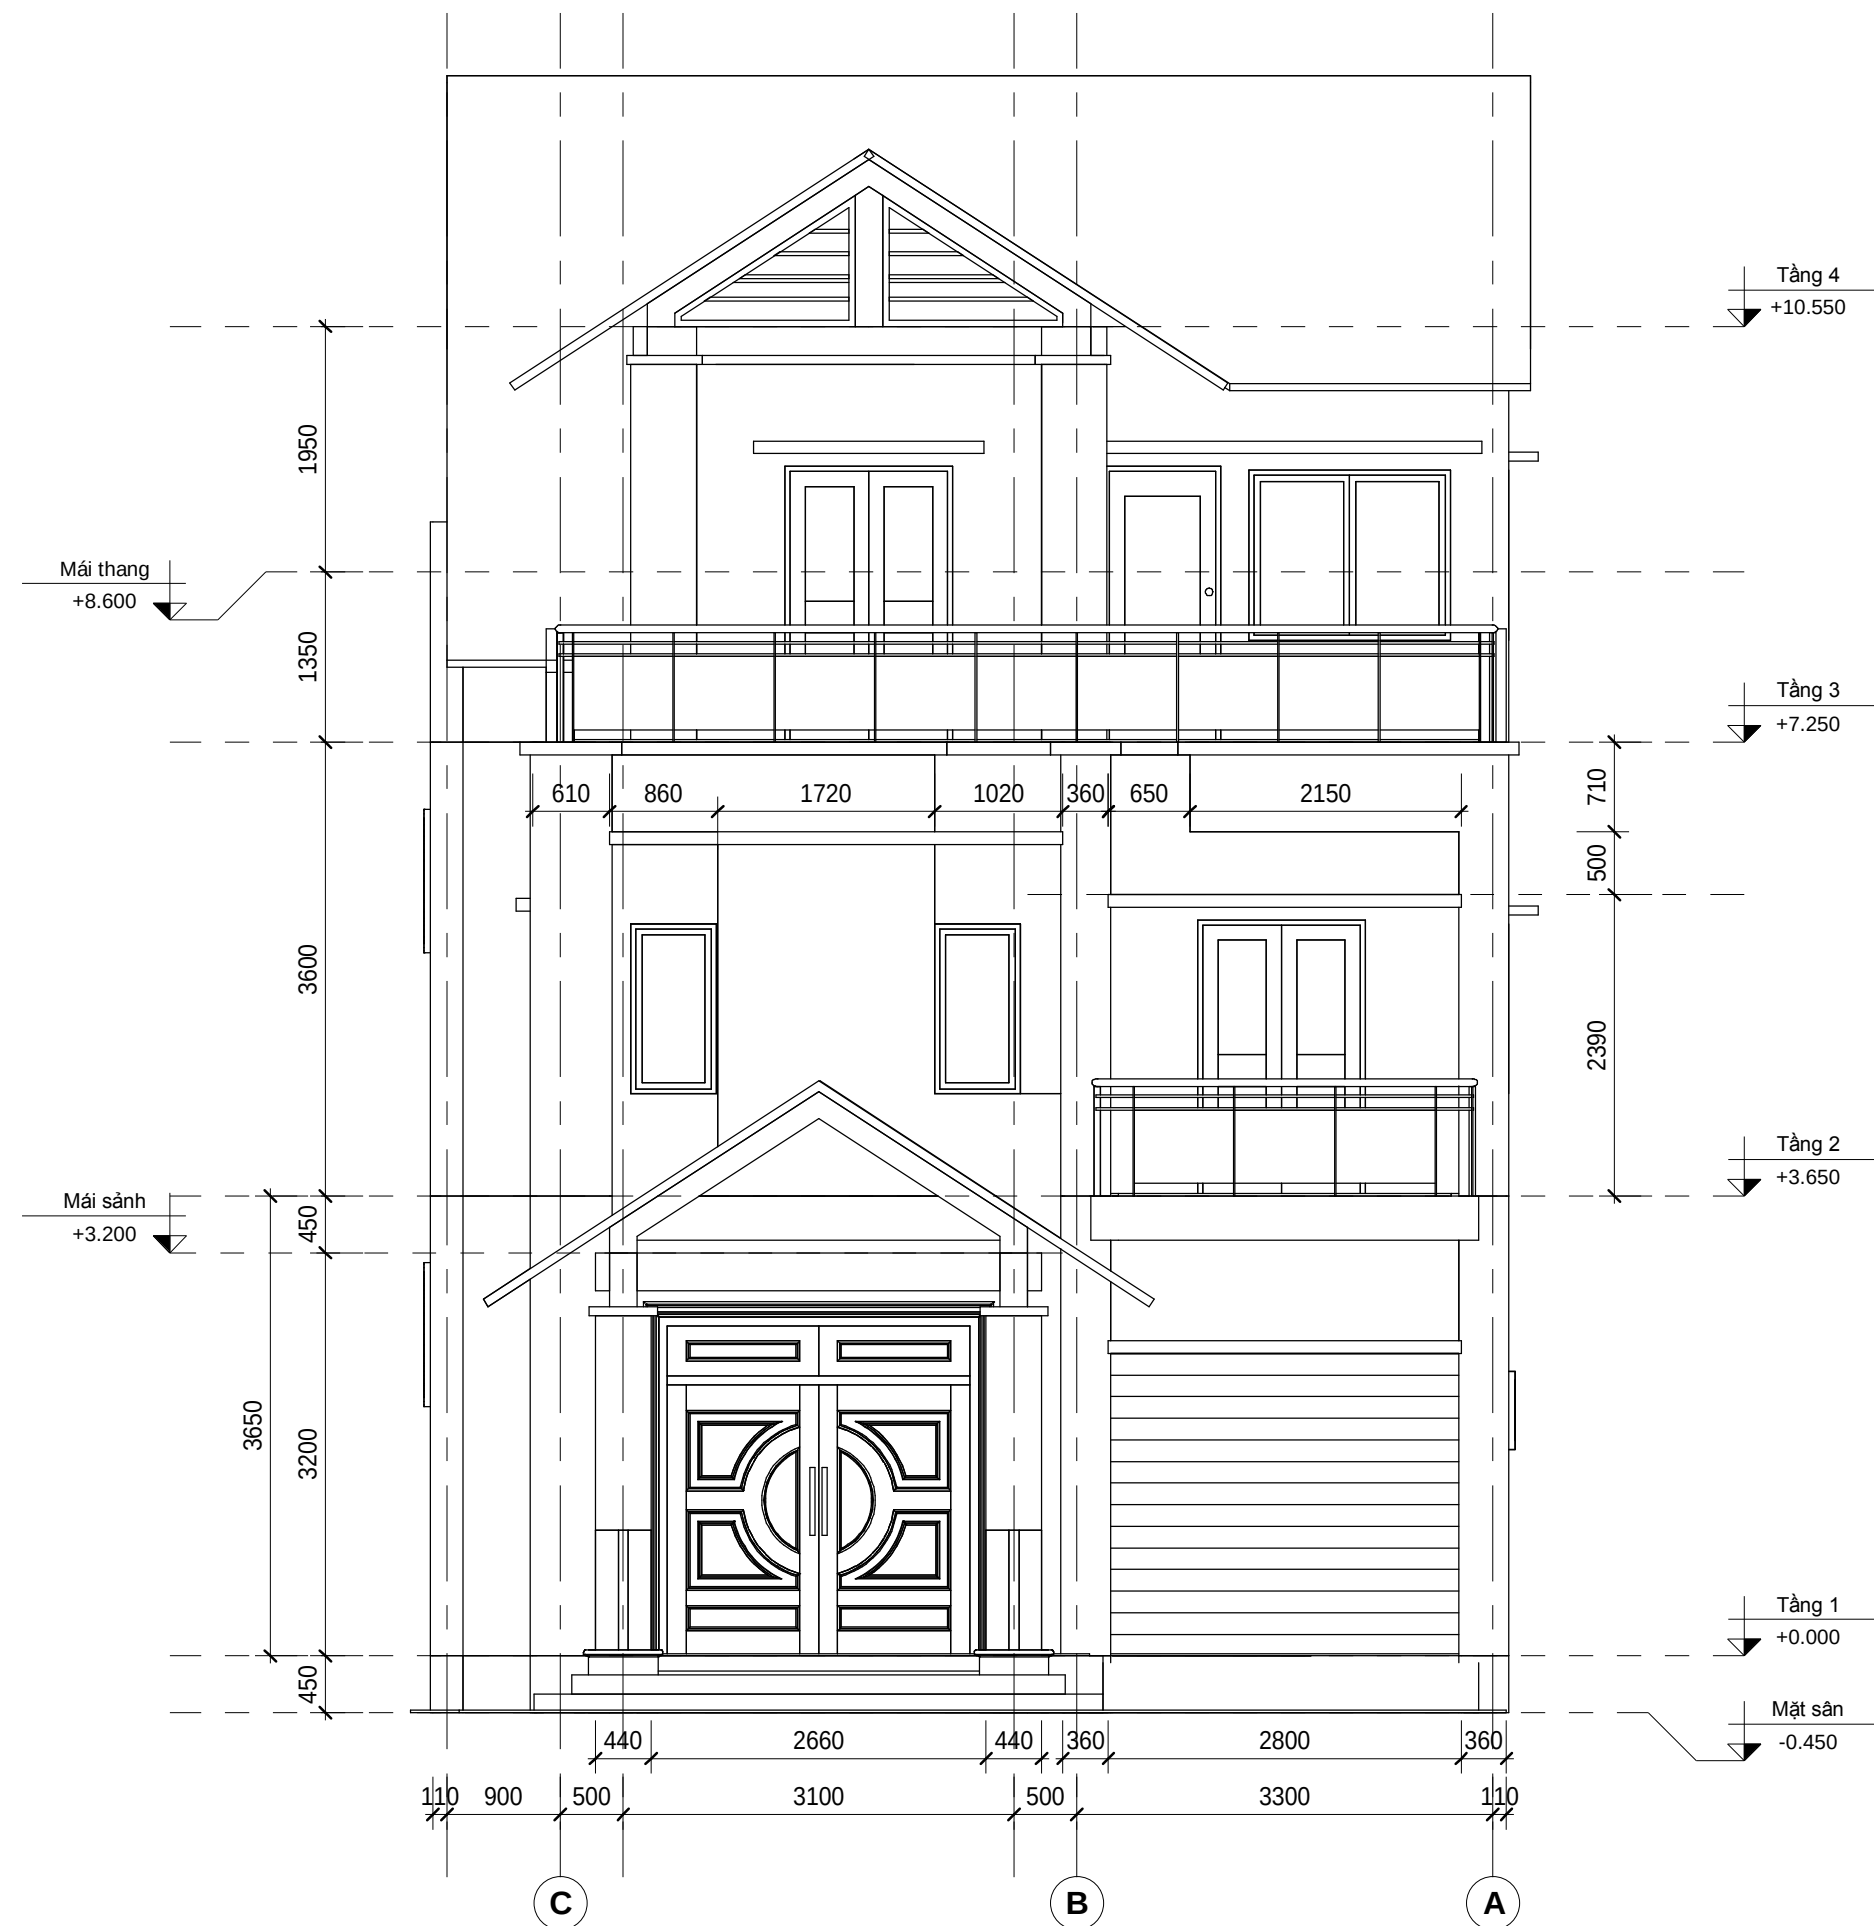


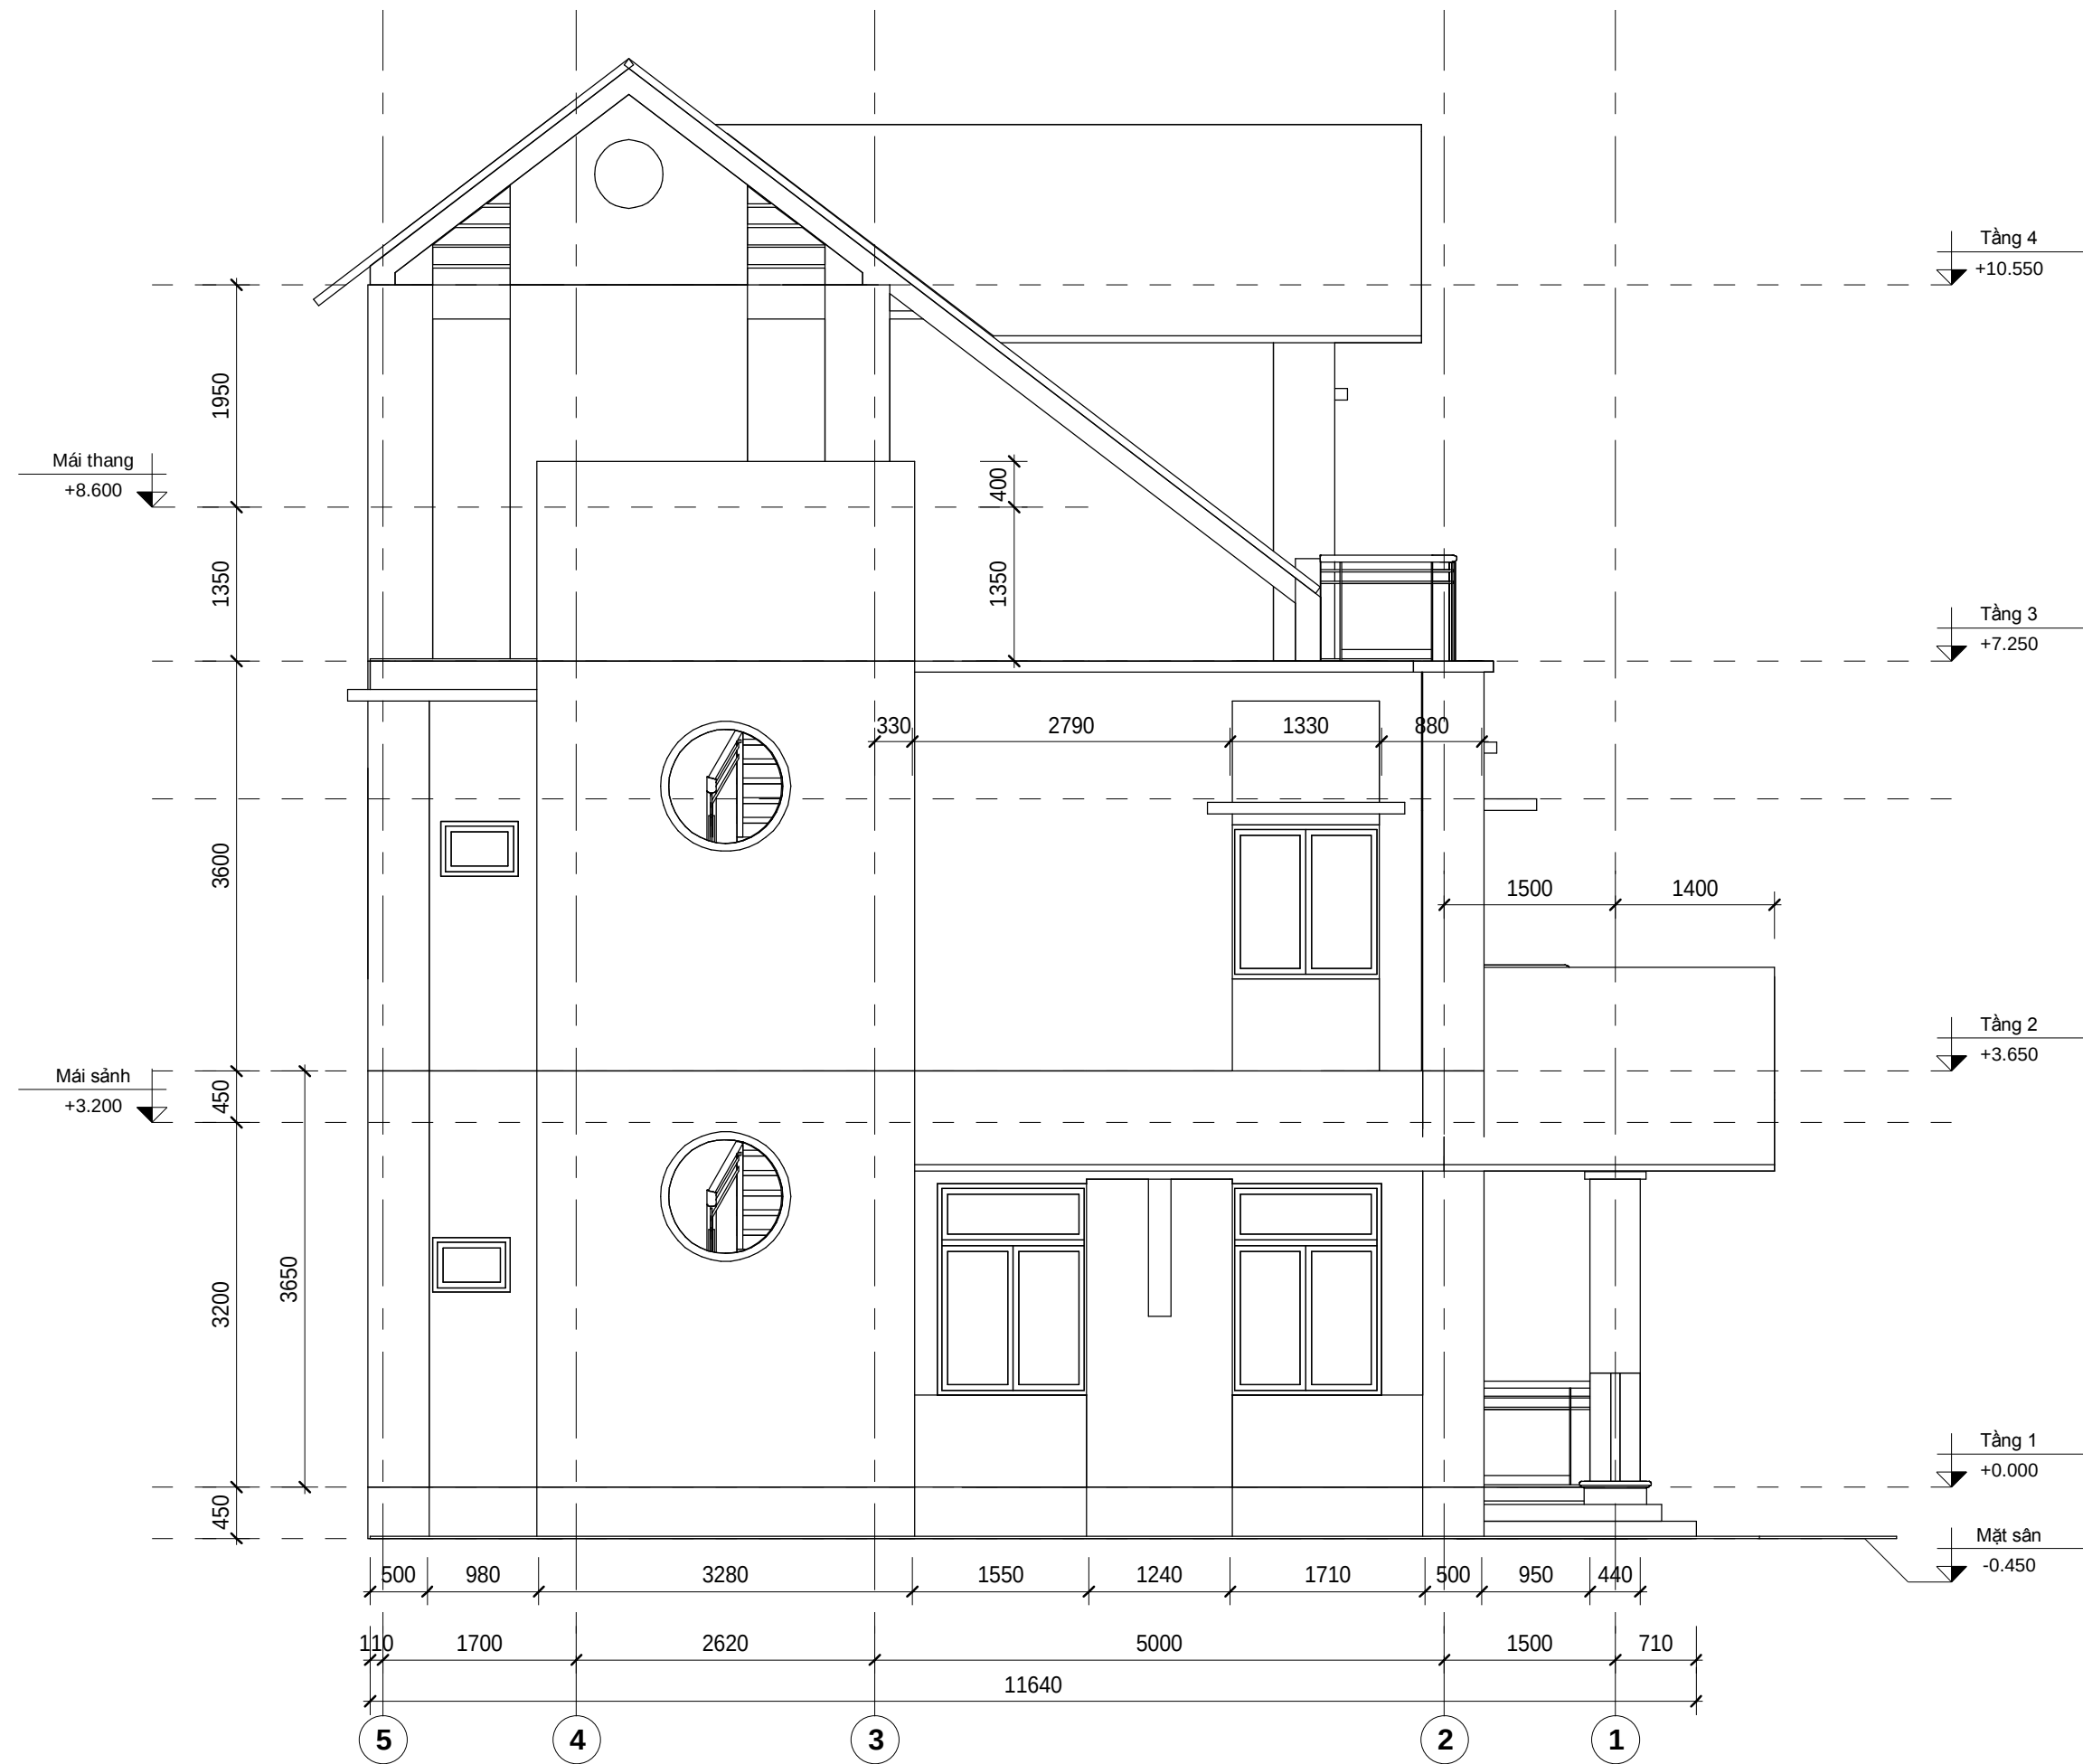


MẶT ĐỨNG TRỤC 5-1

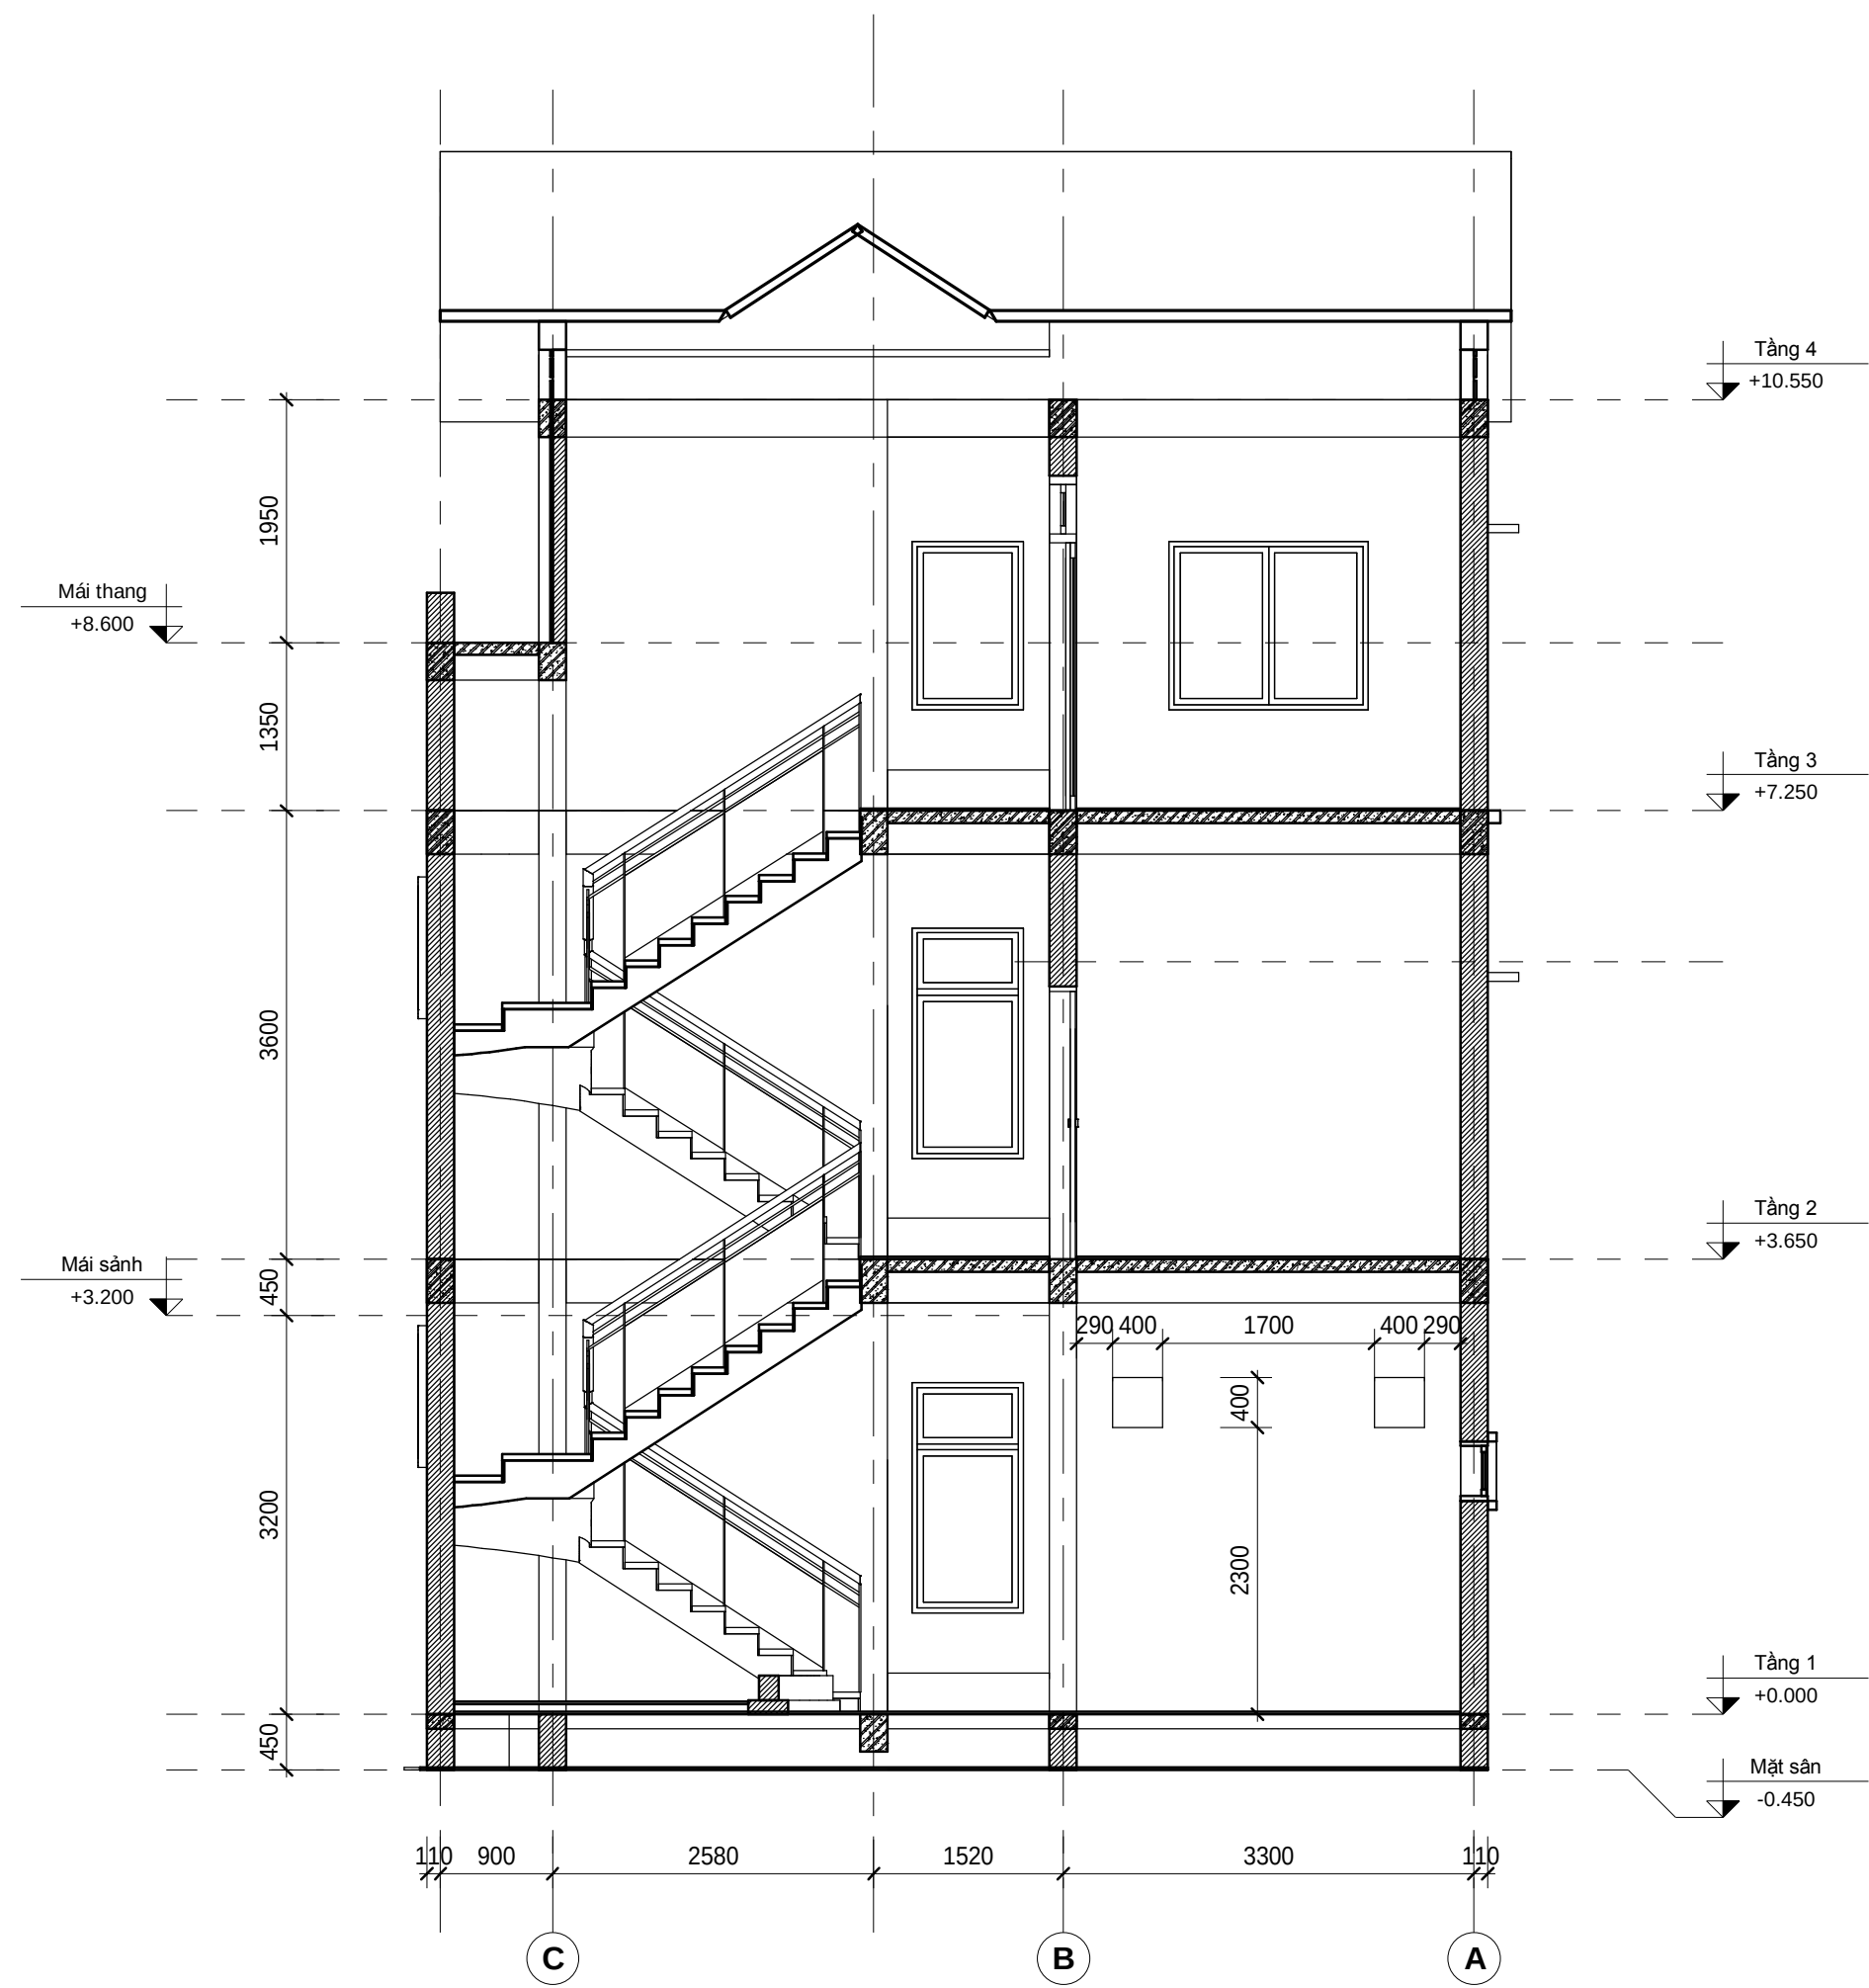

MẶT CẮT A-A

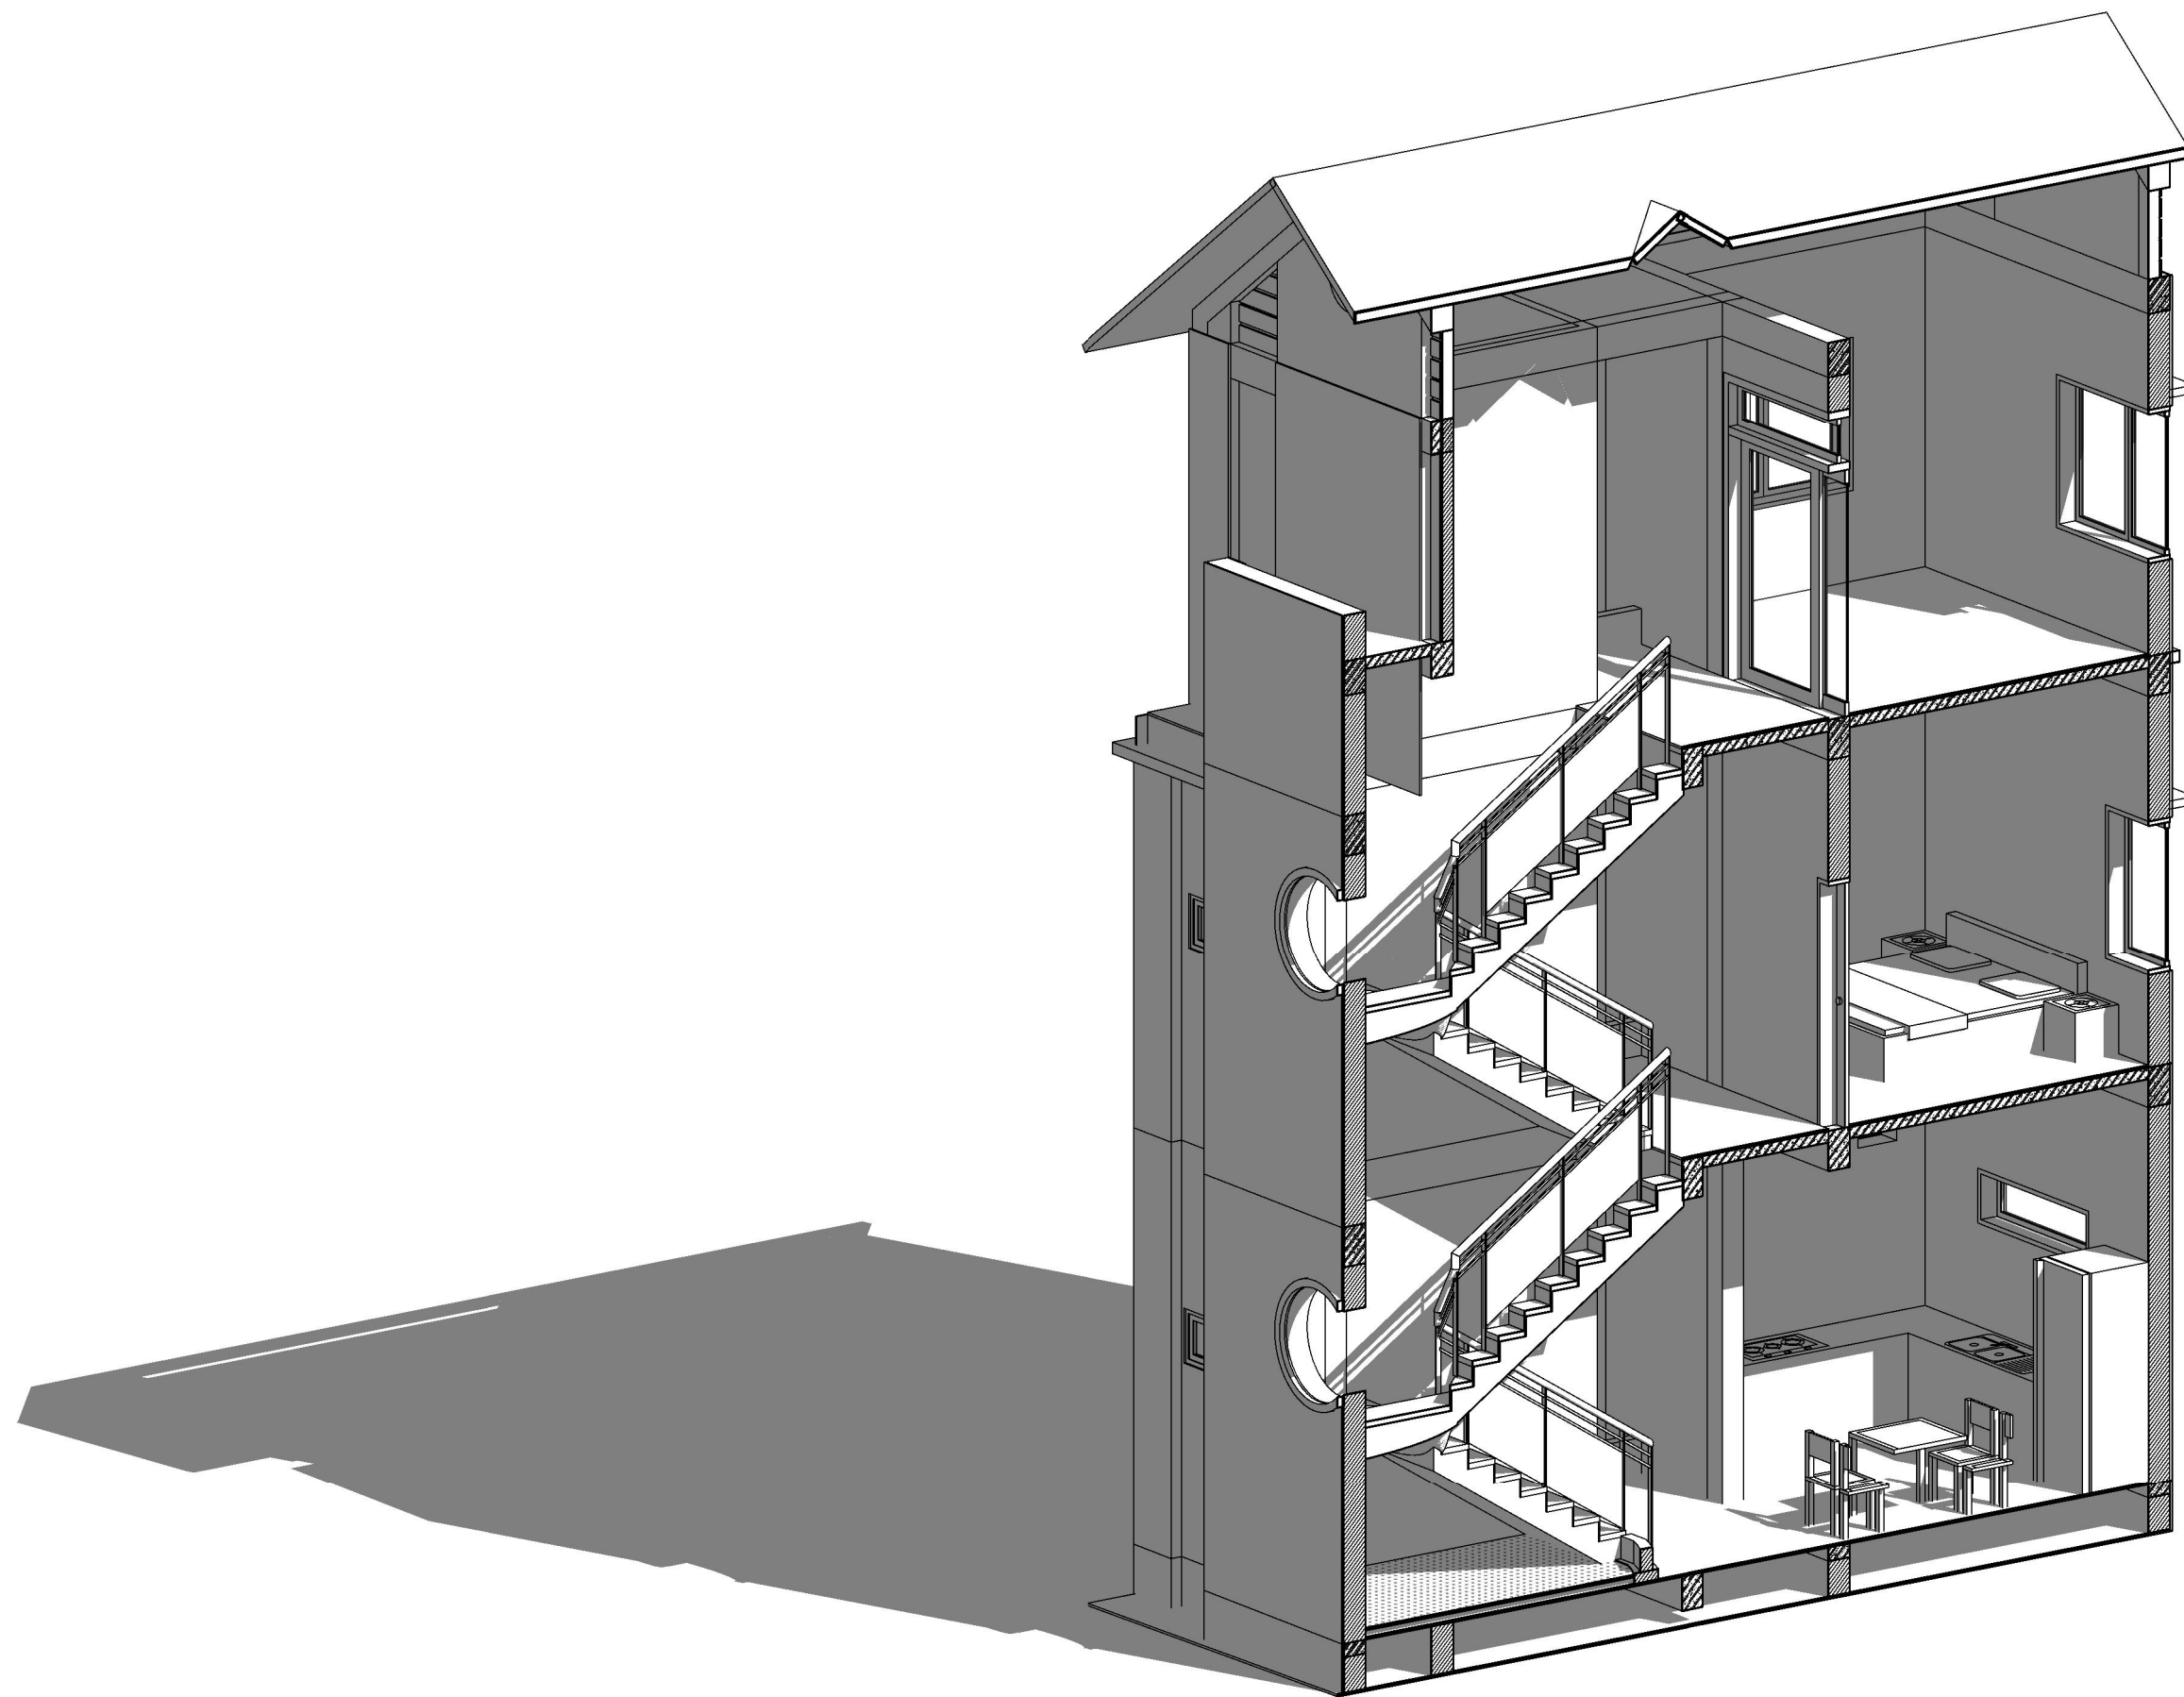

PHỐI CẢNH MẶT CẮT A-A

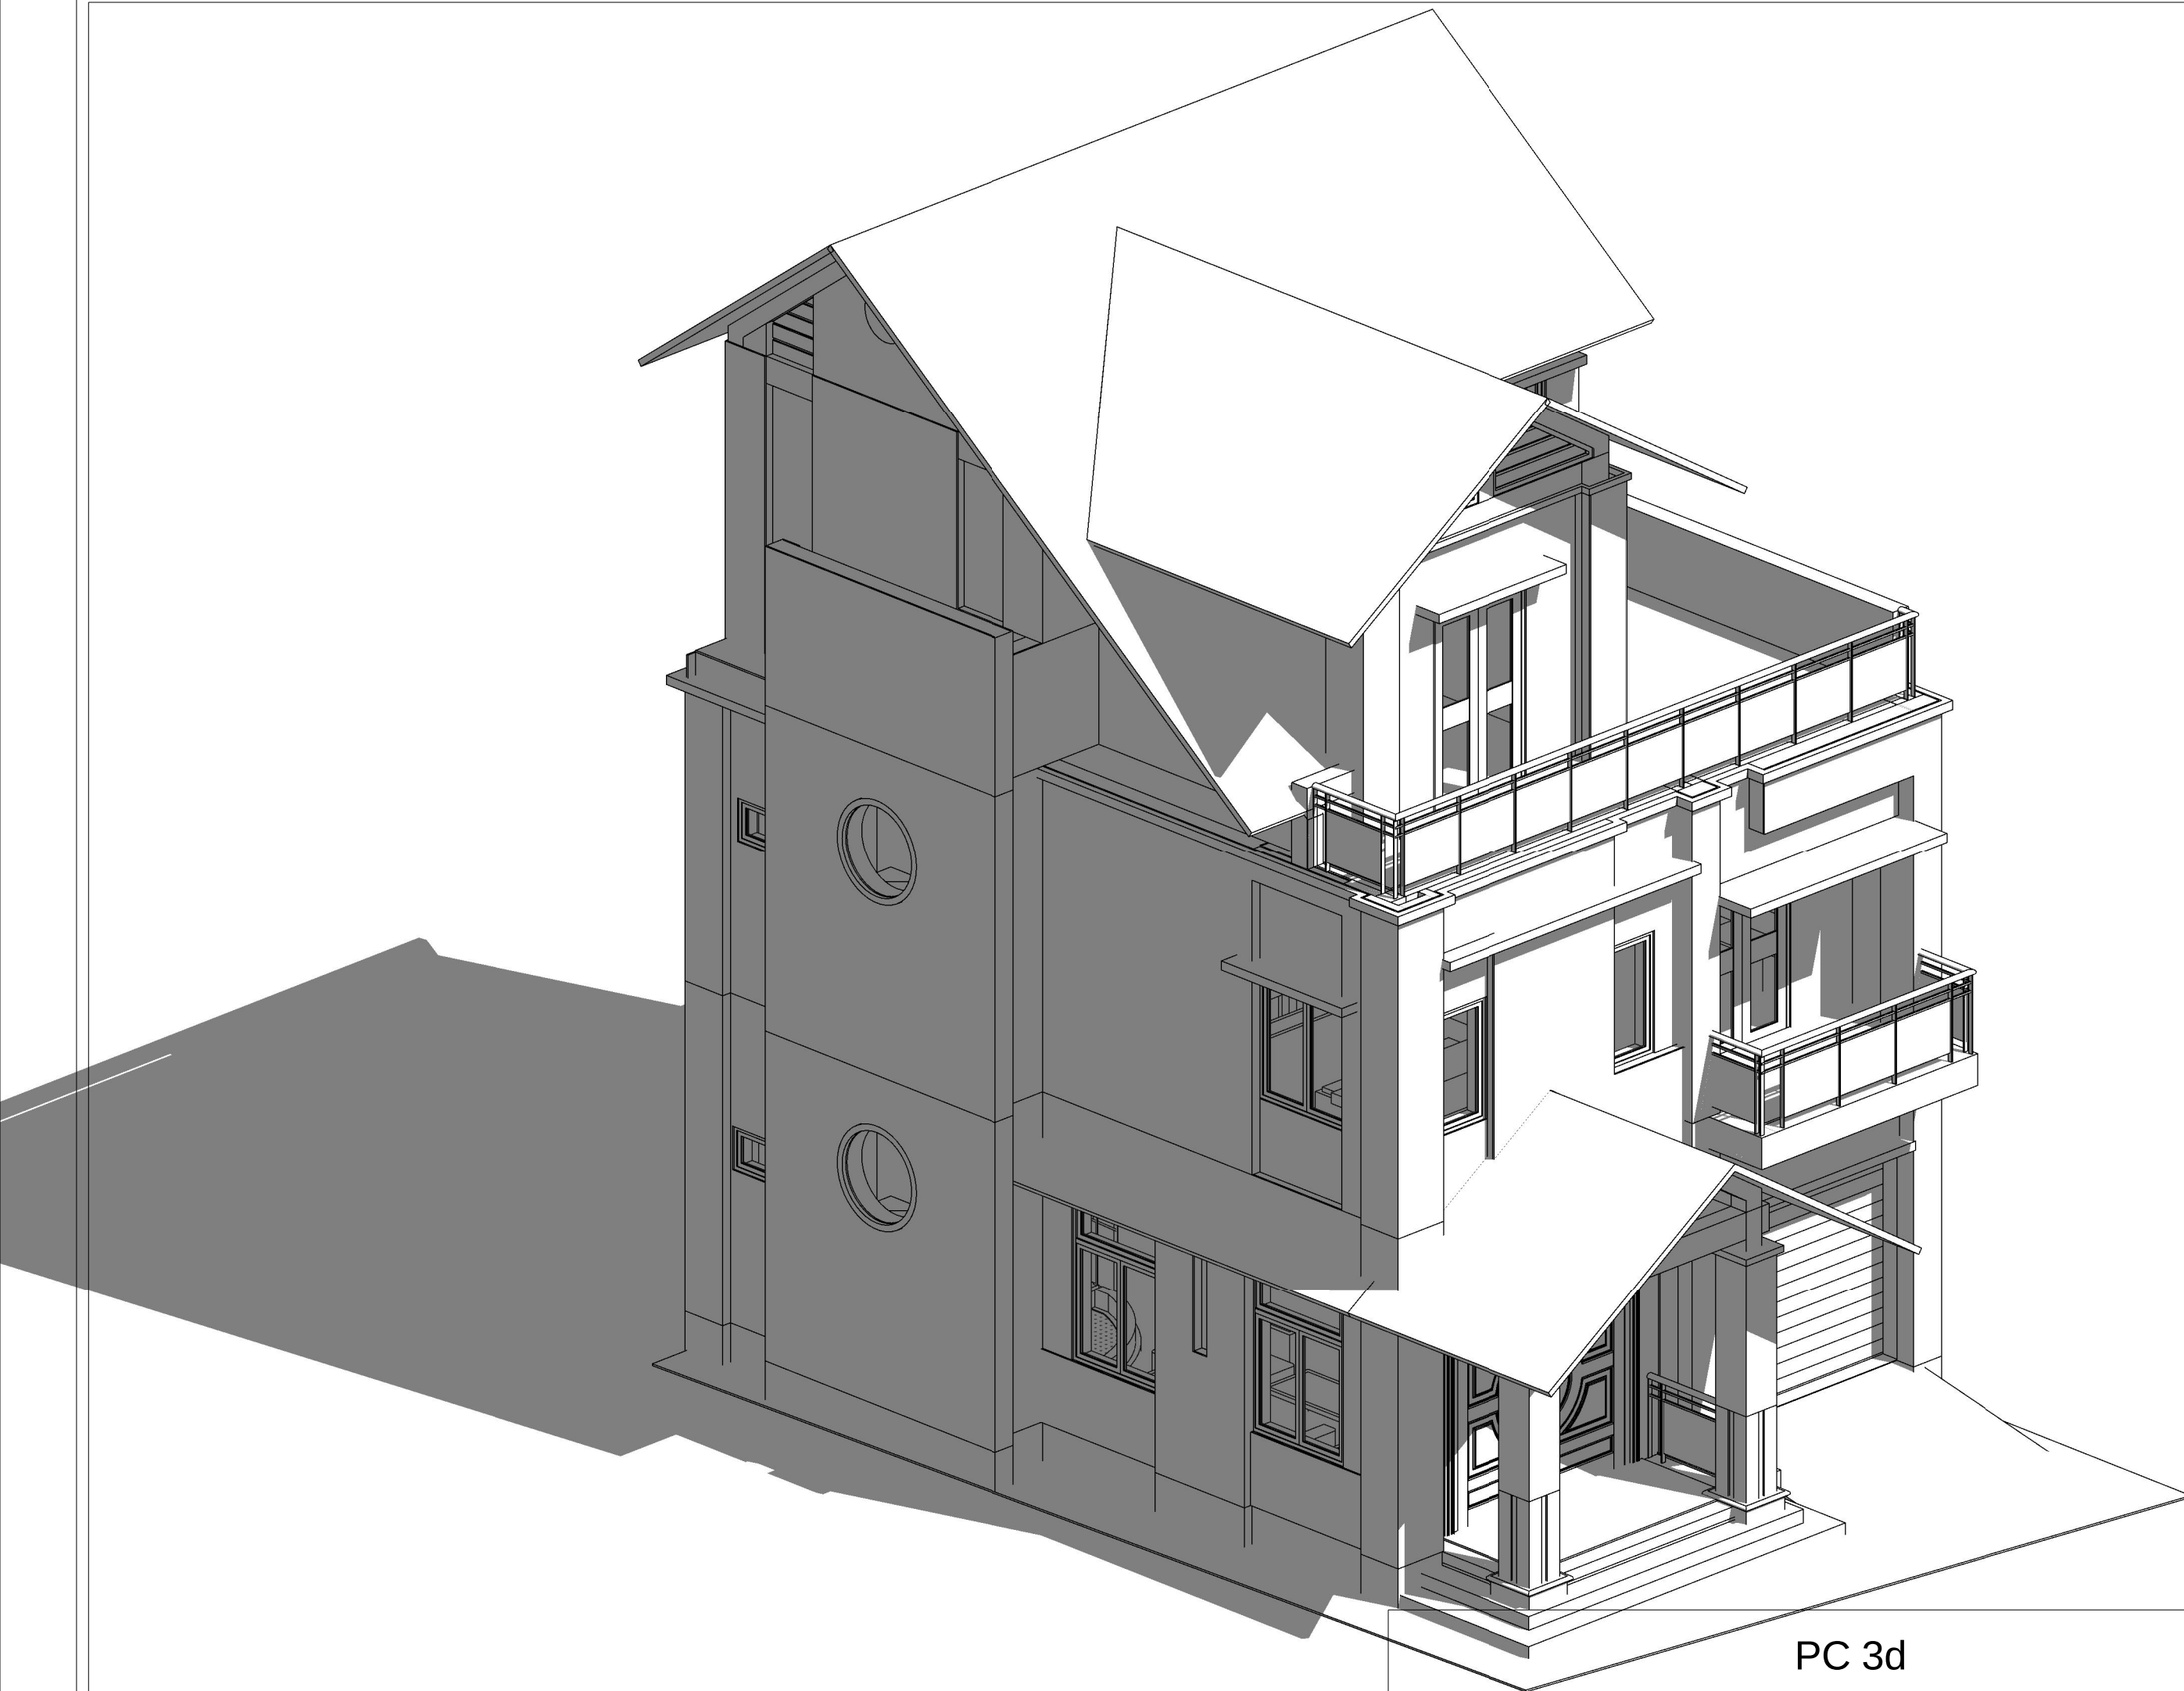

PC 3d

KT-15